


THE DUO DEN

Two people.
One space.
Endless Productivity.

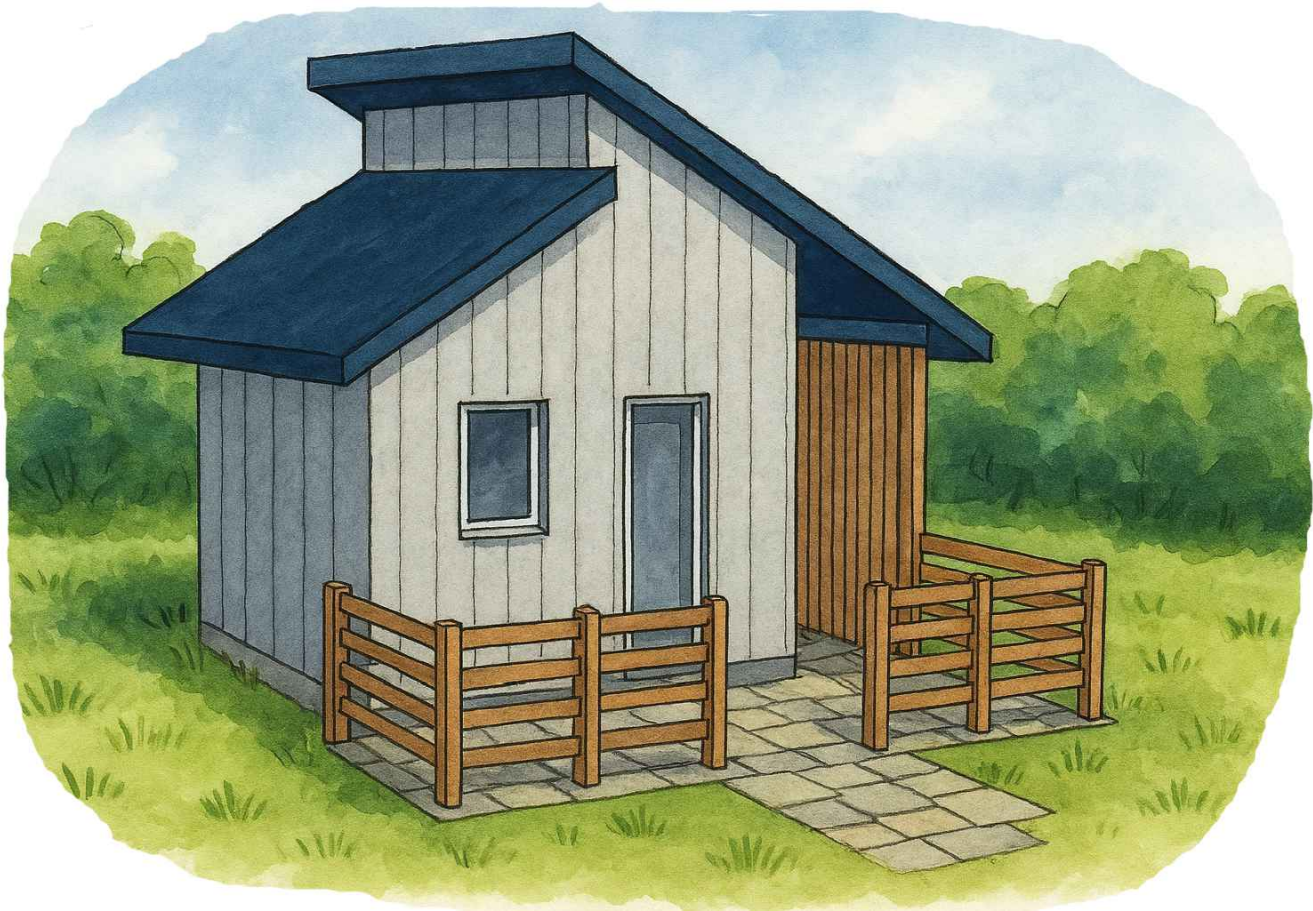

The Duo Den is a compact two-person tiny home crafted to balance productivity and a connection to nature. The structure is oriented to open outward toward surrounding greenery, creating calm views. The interior space sits on a continuous spread footing while the exterior sits on a monolithic slab-on-grade providing stability for the lightweight wood-framed structure. It's casement windows allow residents to control air flow and temperature when required. This balance between privacy and openness makes the Duo Den feel larger than it is, offering both the quiet work space and the calming exposure to natural light and greenery. Thoughtfully designed for two occupants, it provides maximum productivity in a minimal space.

DRAWING INDEX	
AE001	ISOMETRIC VIEW
AE002	SITE PLAN
AE101	FLOOR PLAN 1
AE102	FLOOR PLAN 2
AE103	ROOF PLAN
AE201	SOUTHEAST ELEVATION
AE202	NORTHEAST ELEVATION
AE203	SOUTHWEST ELEVATION
AE204	NORTHWEST ELEVATION
AE301	SOUTHEAST SECTION
AE302	BED SECTION
AE303	SLIDING DOOR SECTION
AE401	FOUNDATION WALL DETAIL
AE402	MONOLITHIC SLAB DETAIL
AE403	WALL DETAIL
AE404	WINDOW DETAIL
AE405	SLIDING DOOR DETAIL
AE406	ROOF DETAIL
AE407	FENCE POST DETAIL
AE408	LOUVER DETAIL



190 Westmount Rd N,
Waterloo, ON N2L 3G5



THE DUO DEN

TINY RETREAT PROJECT


COVER PAGE

12/05/2025

GROUP 8

mm

AE000

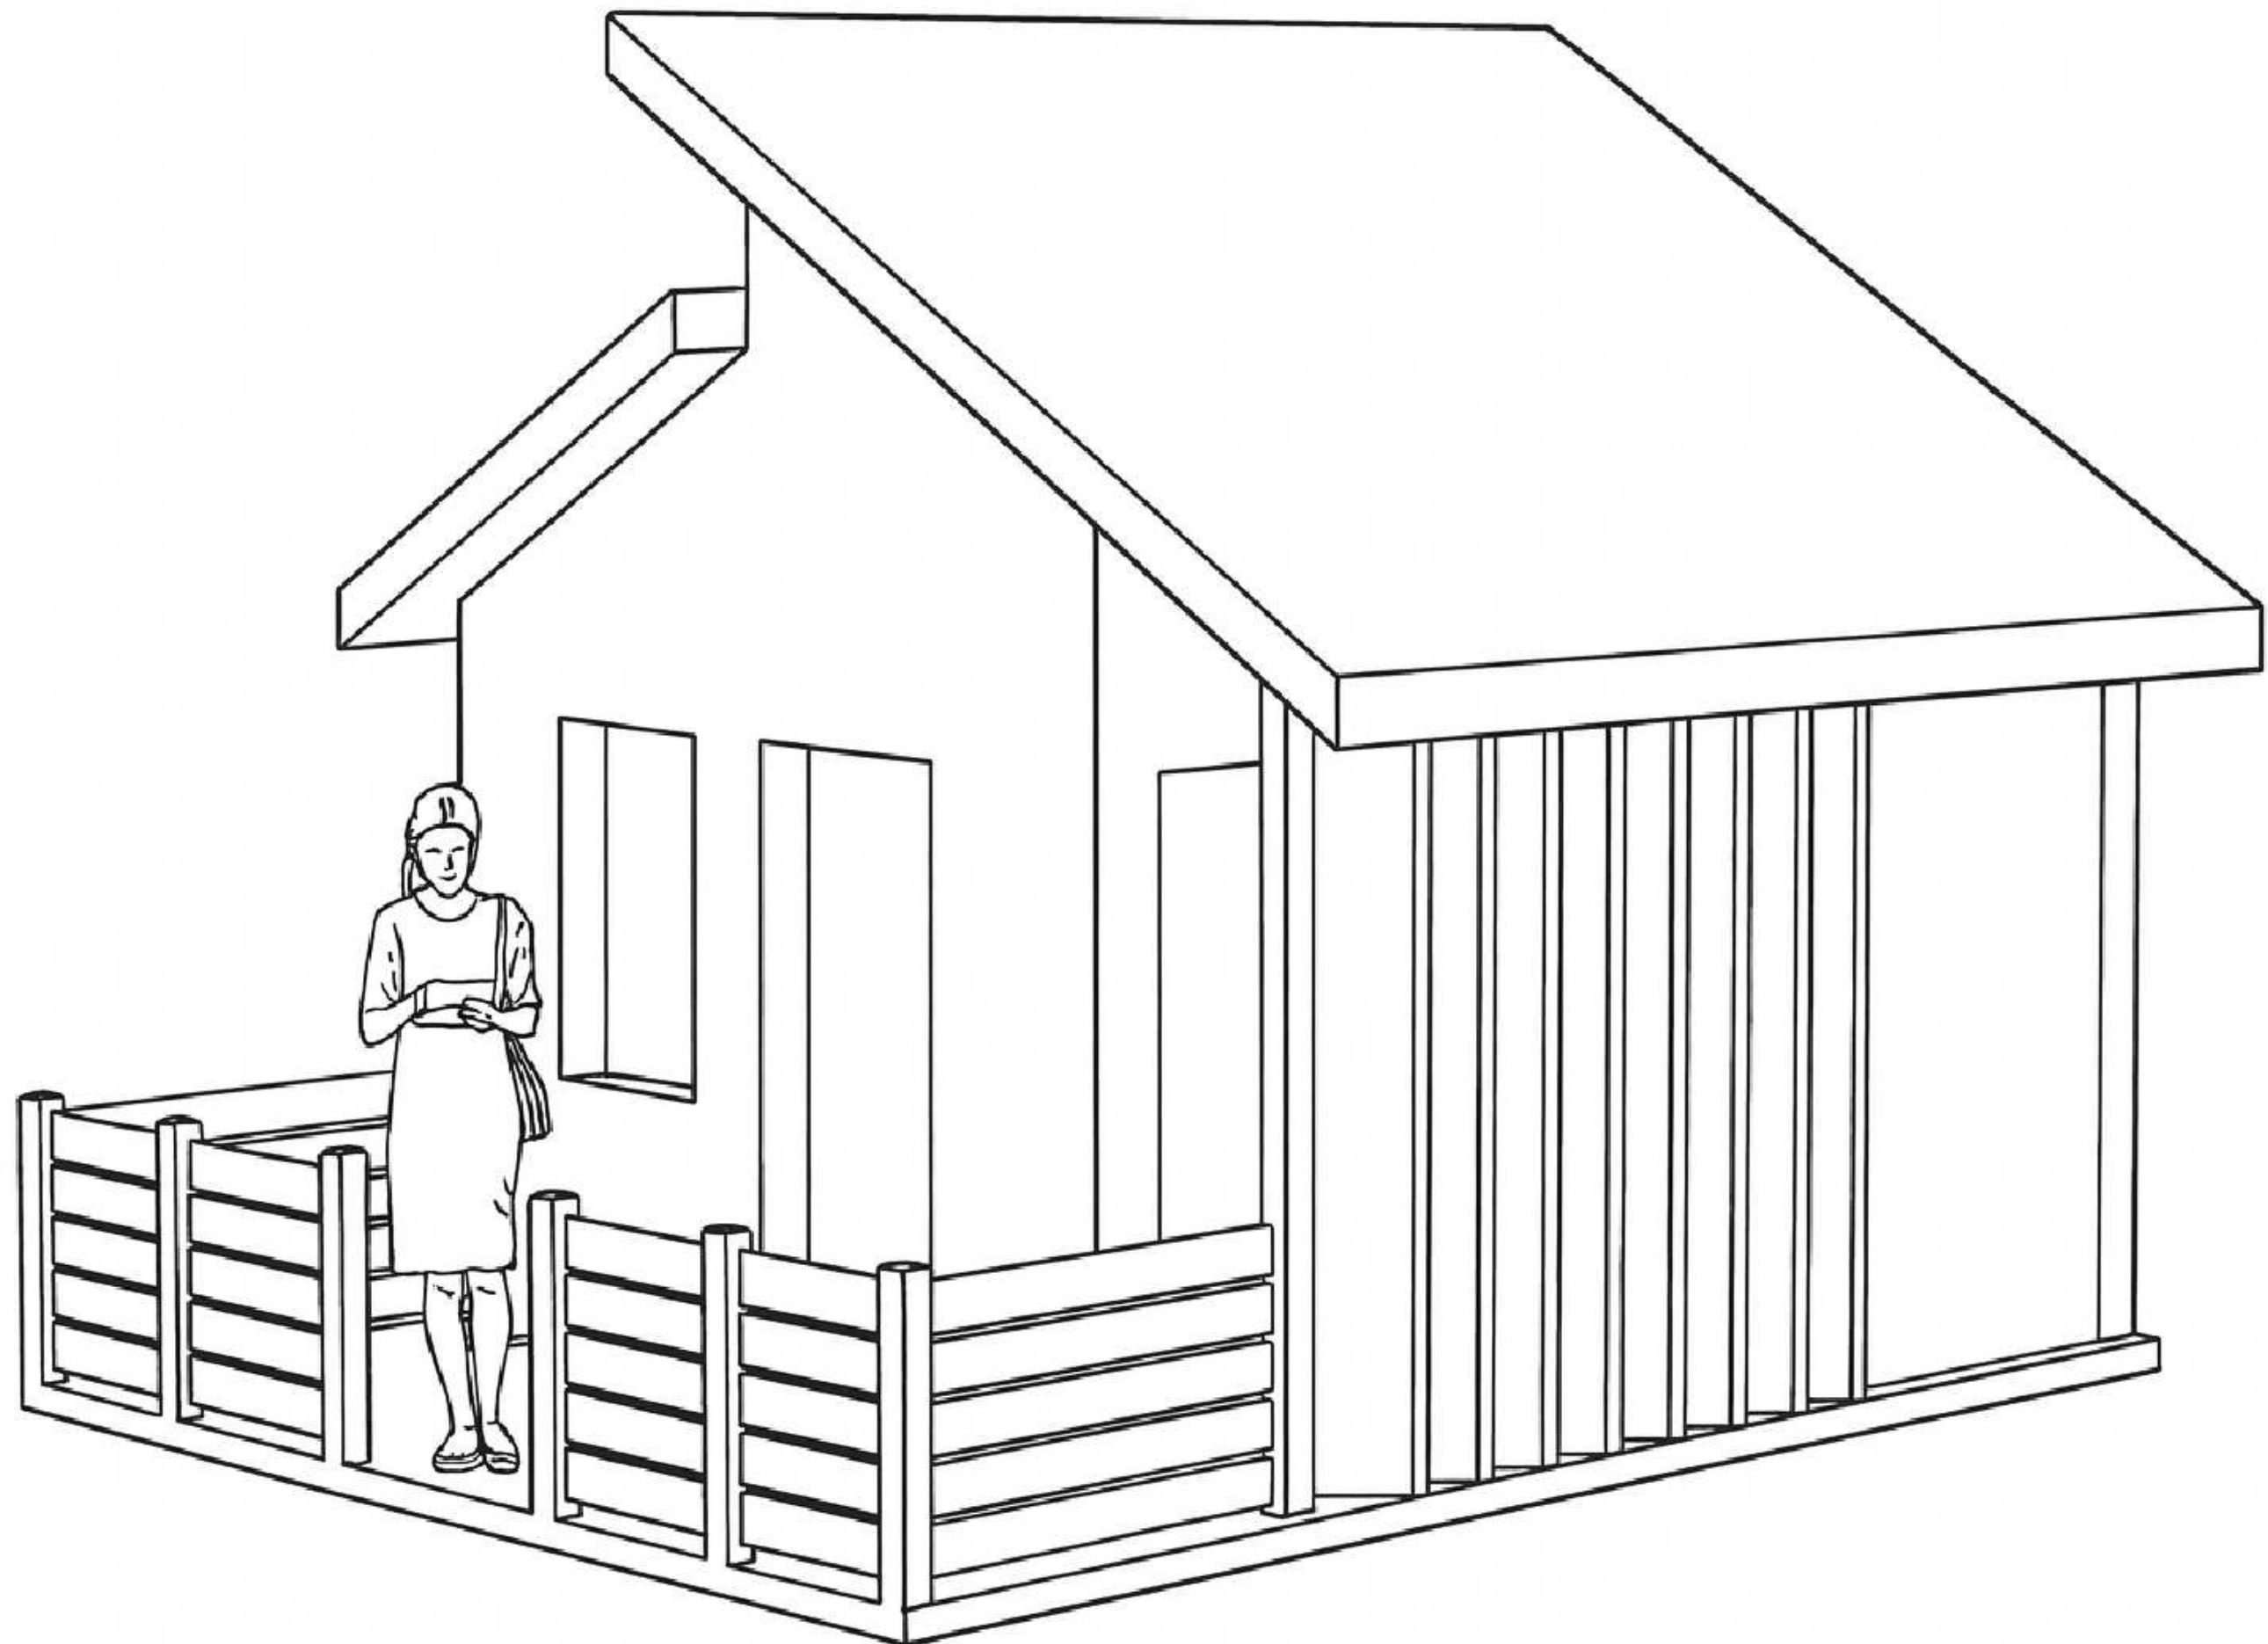

190 Westmount Rd N,
Waterloo, ON N2L 3G5



TINY RETREAT
PROJECT

3D VIEW




12/05/2025

mm

GROUP 8

AE001

1:20

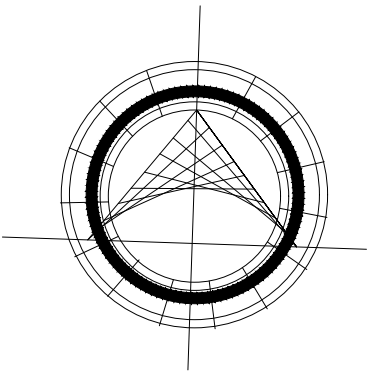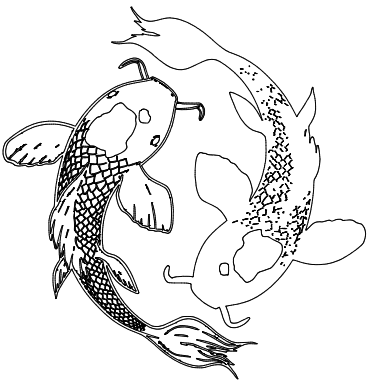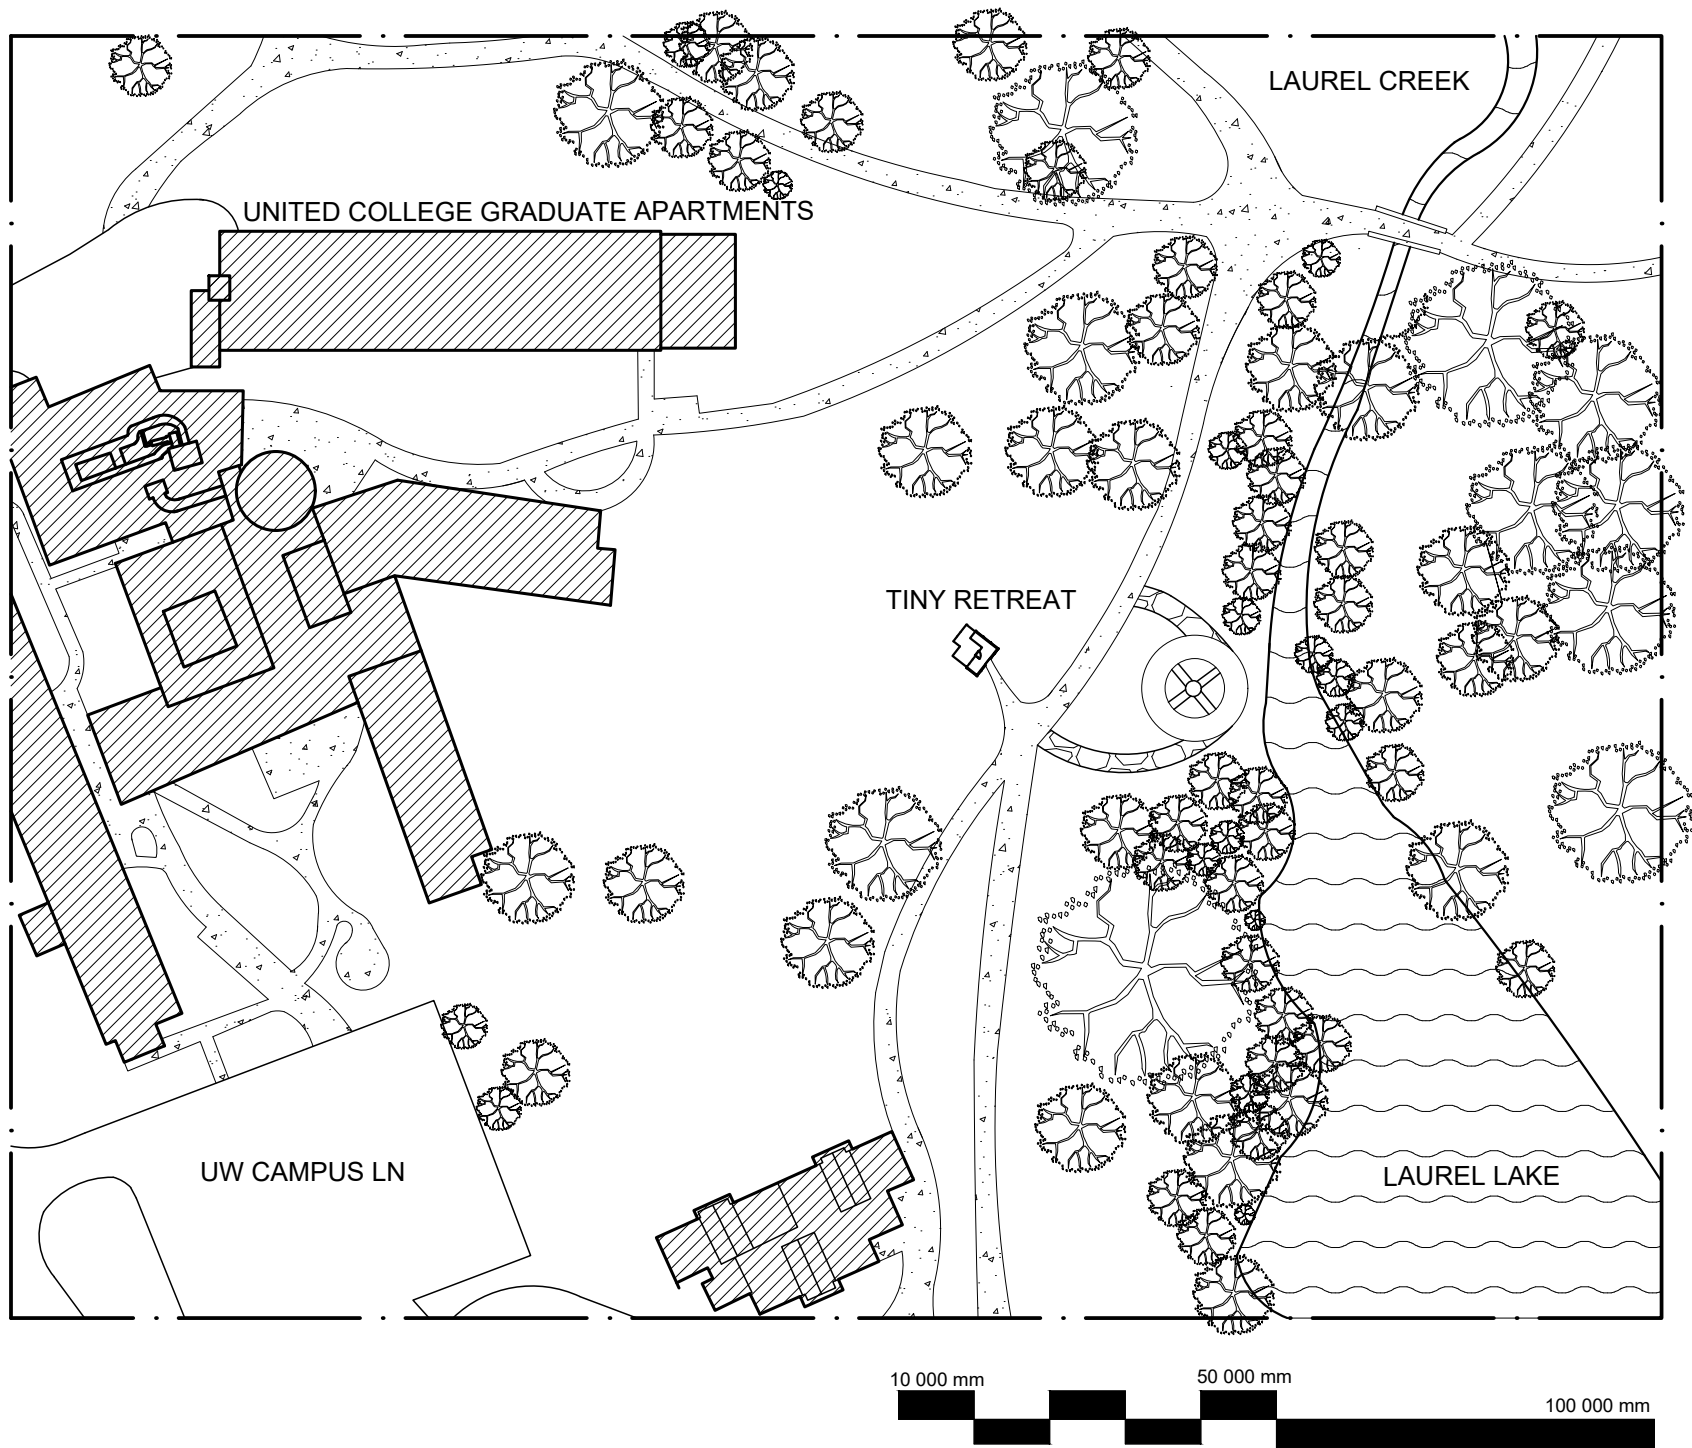

TINY RETREAT
PROJECT

UNITED SITE
PLAN

12/05/2025

mm



GROUP 8

1:1000

AE002

1

FLOOR PLAN
1:25

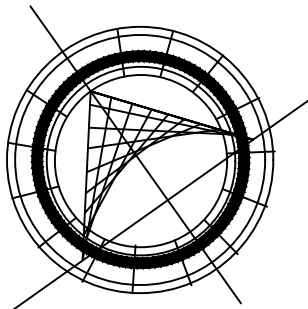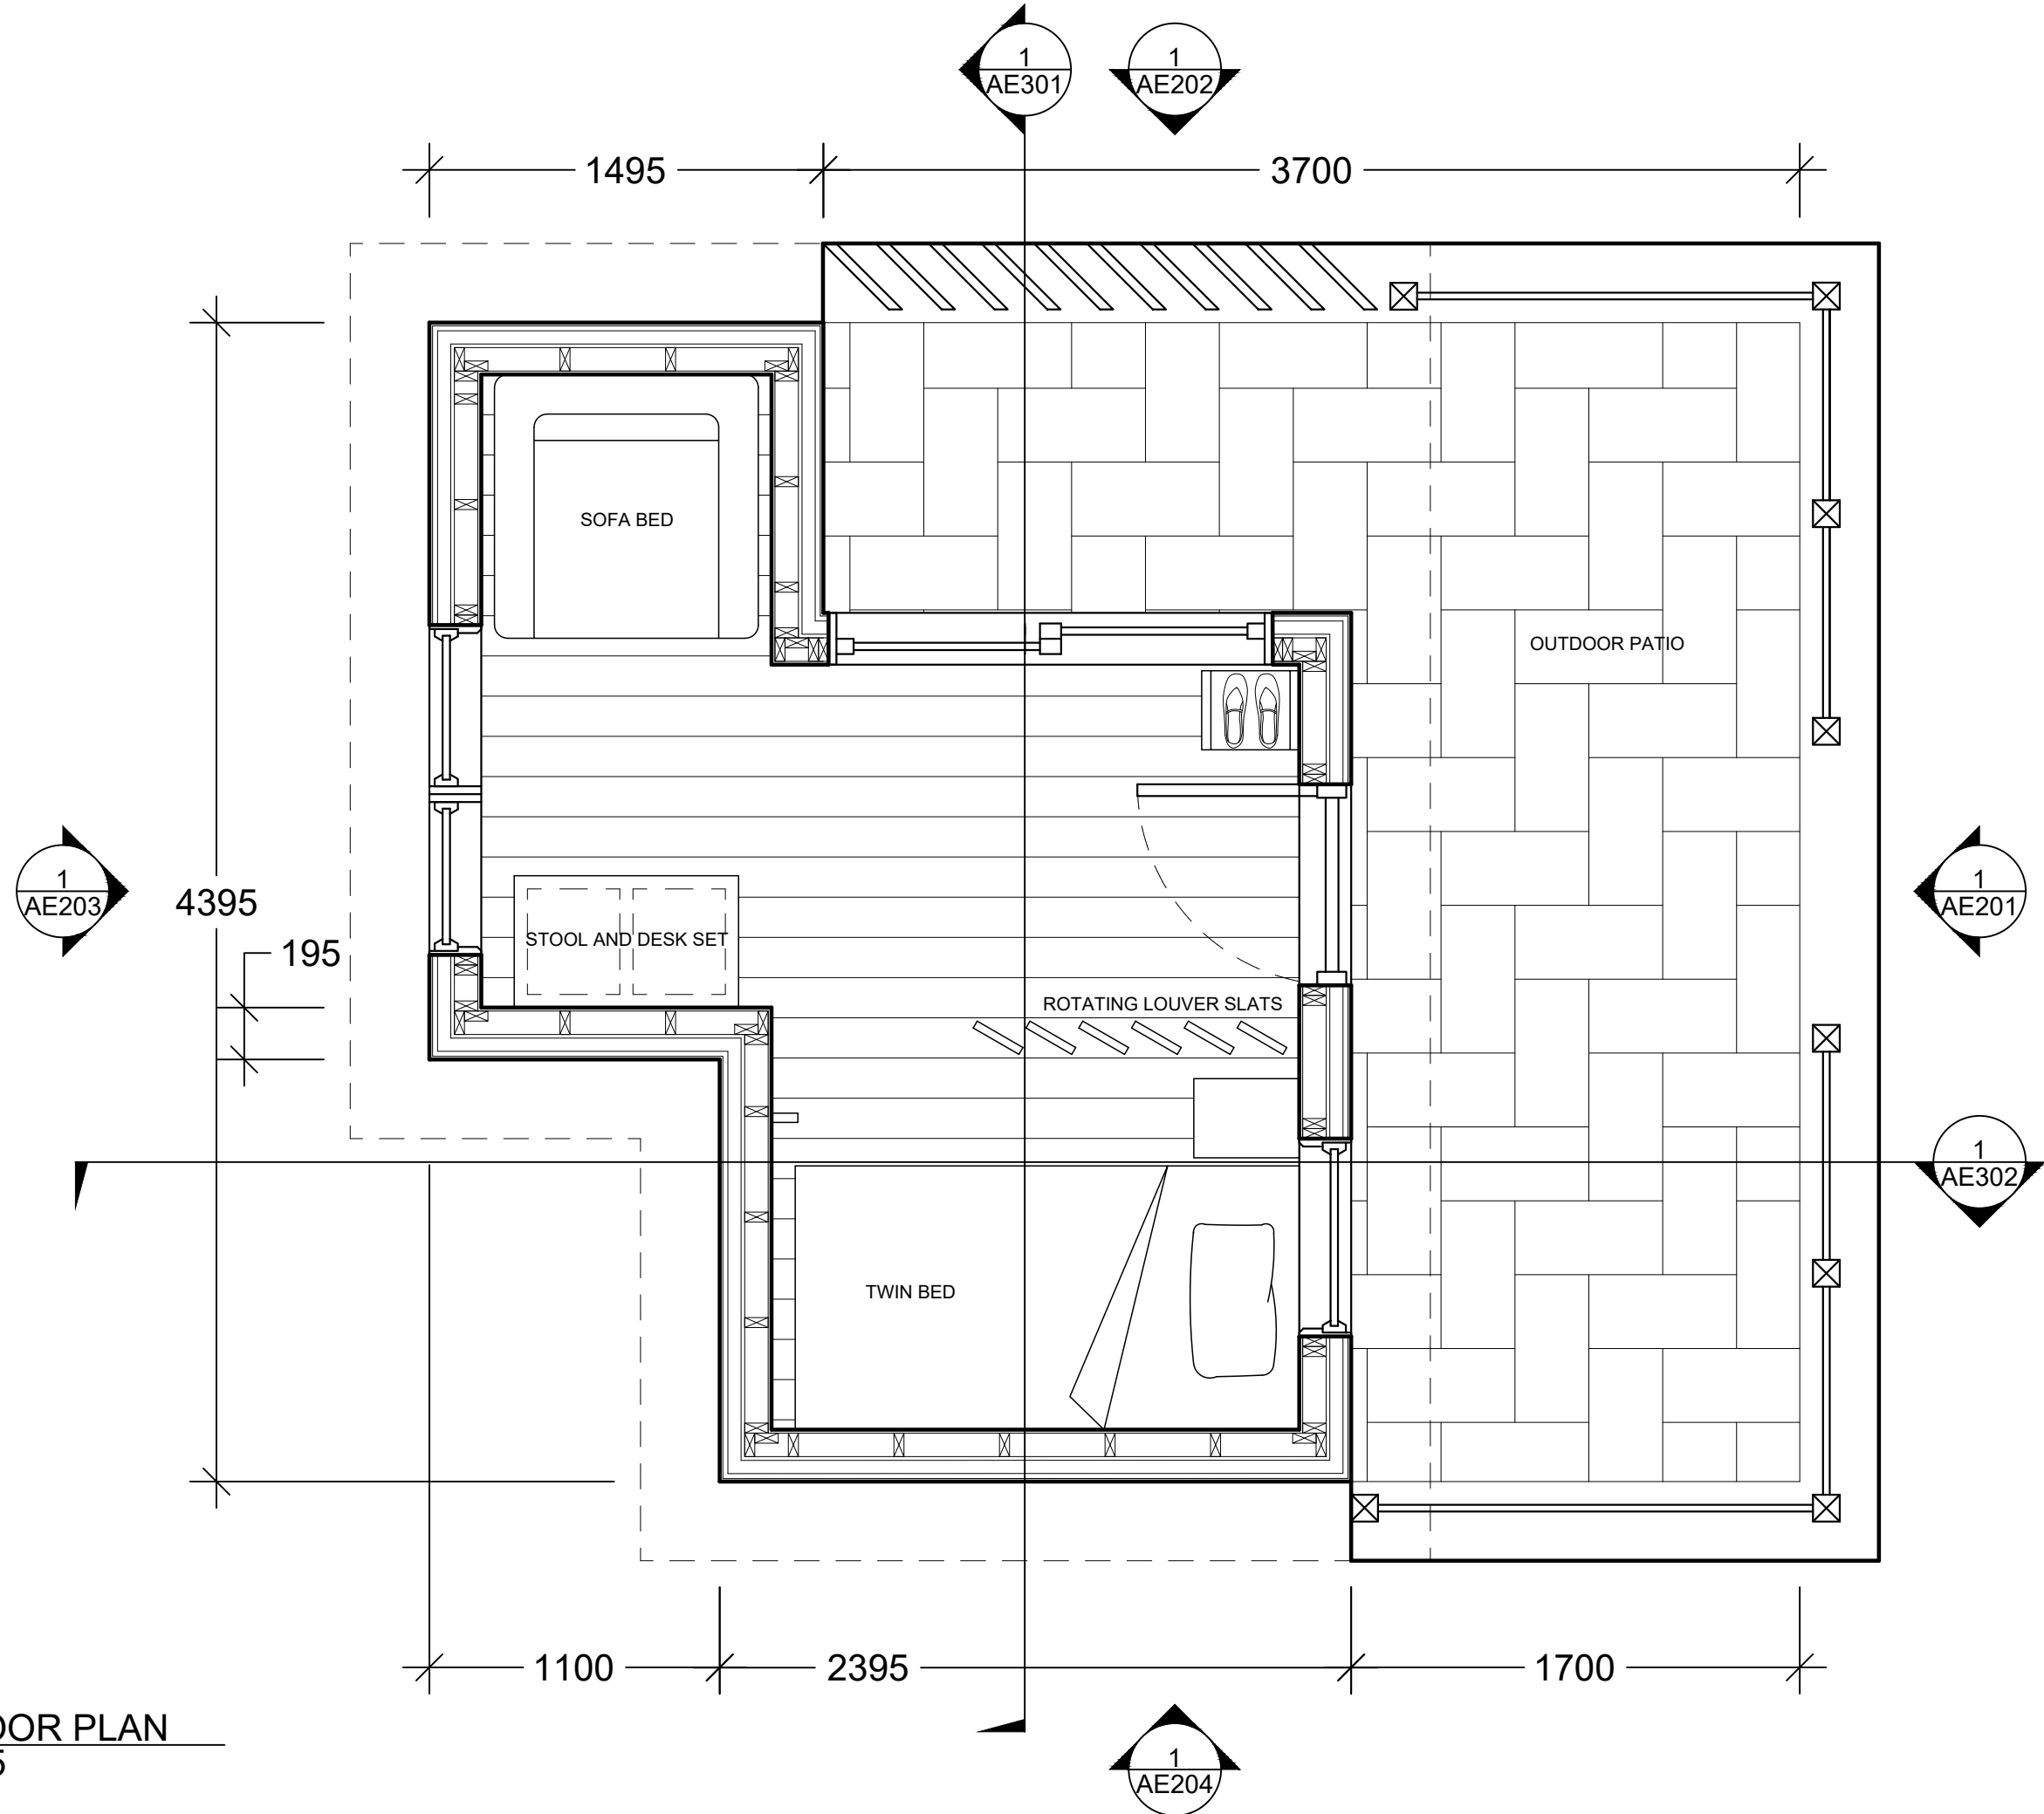

TINY RETREAT
PROJECT

FLOOR PLAN


12/05/2025

mm

GROUP 8

1:25

AE101

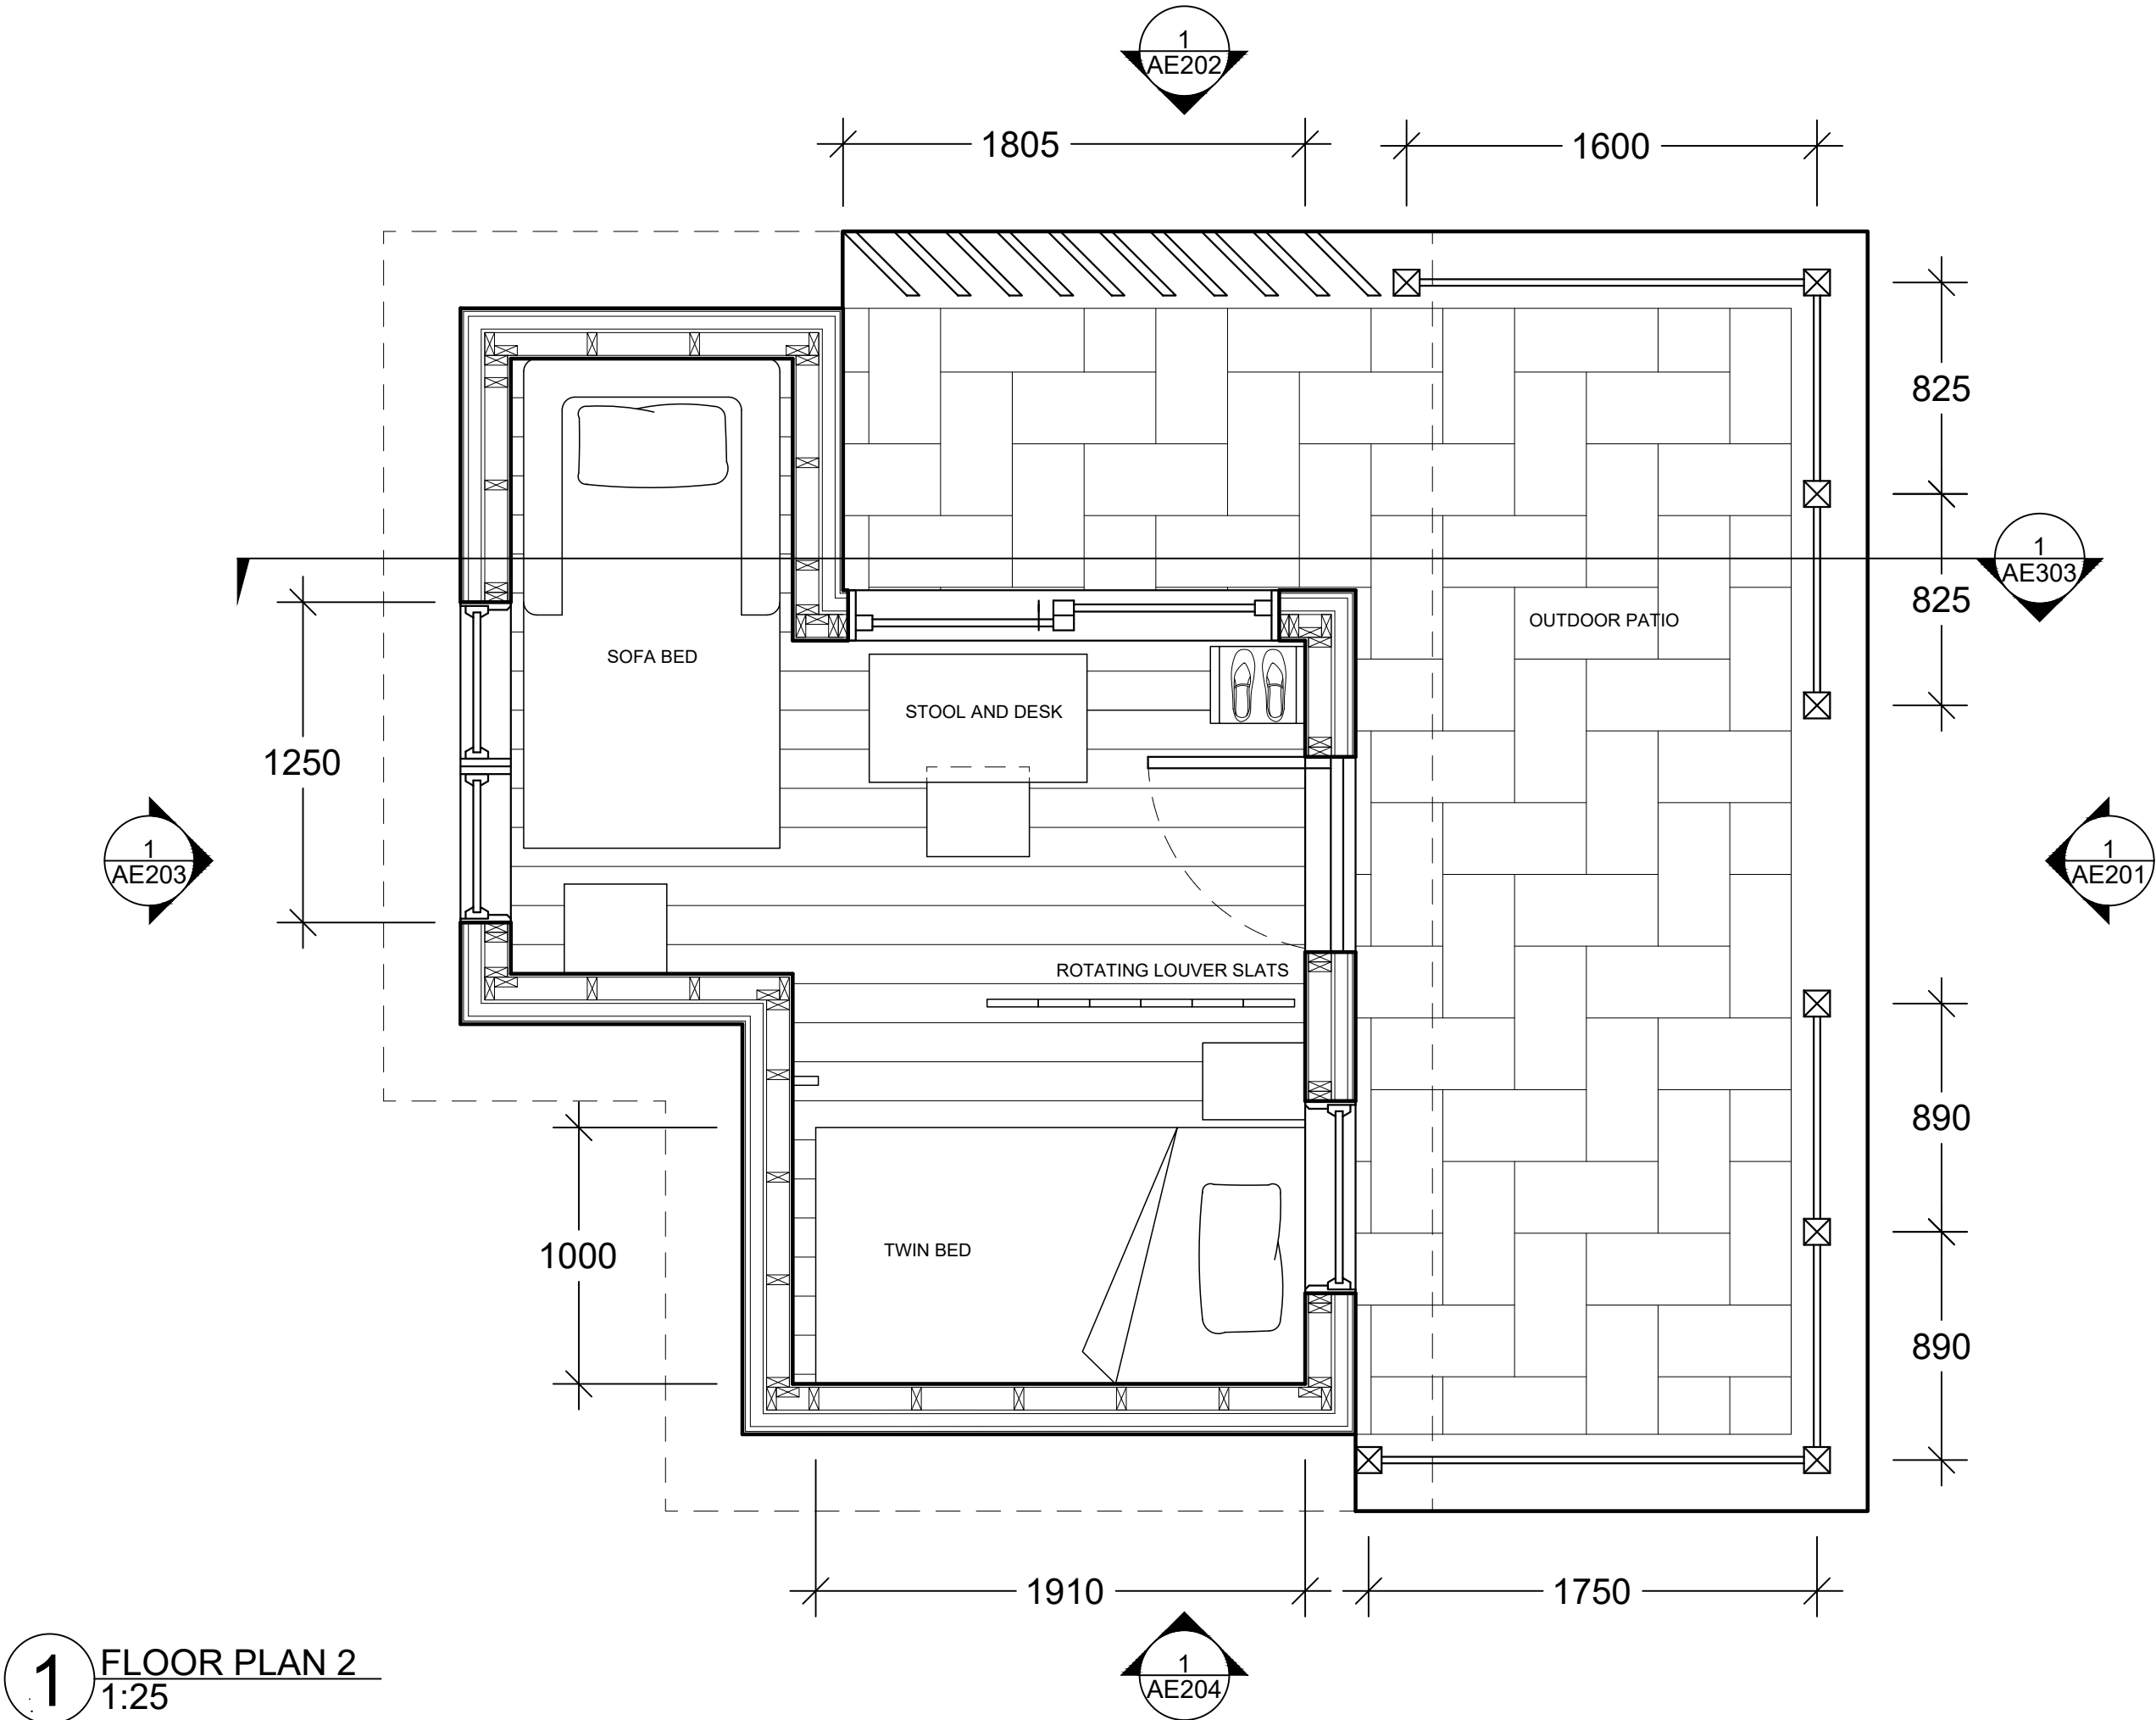


1 FLOOR PLAN 2
1:25



UNIVERSITY OF
WATERLOO

190 Westmount Rd N,
Waterloo, ON N2L 3G5



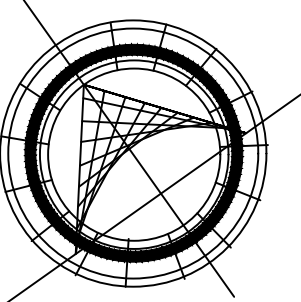



TINY RETREAT
PROJECT

FLOOR PLAN
ALTERNATE
LAYOUT

12/05/2025	mm
GROUP 8	
1:25	AE102

1

ROOF PLAN
1:25

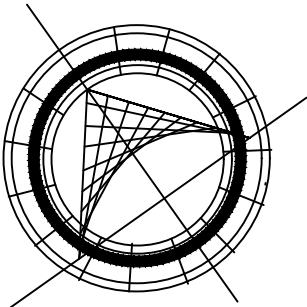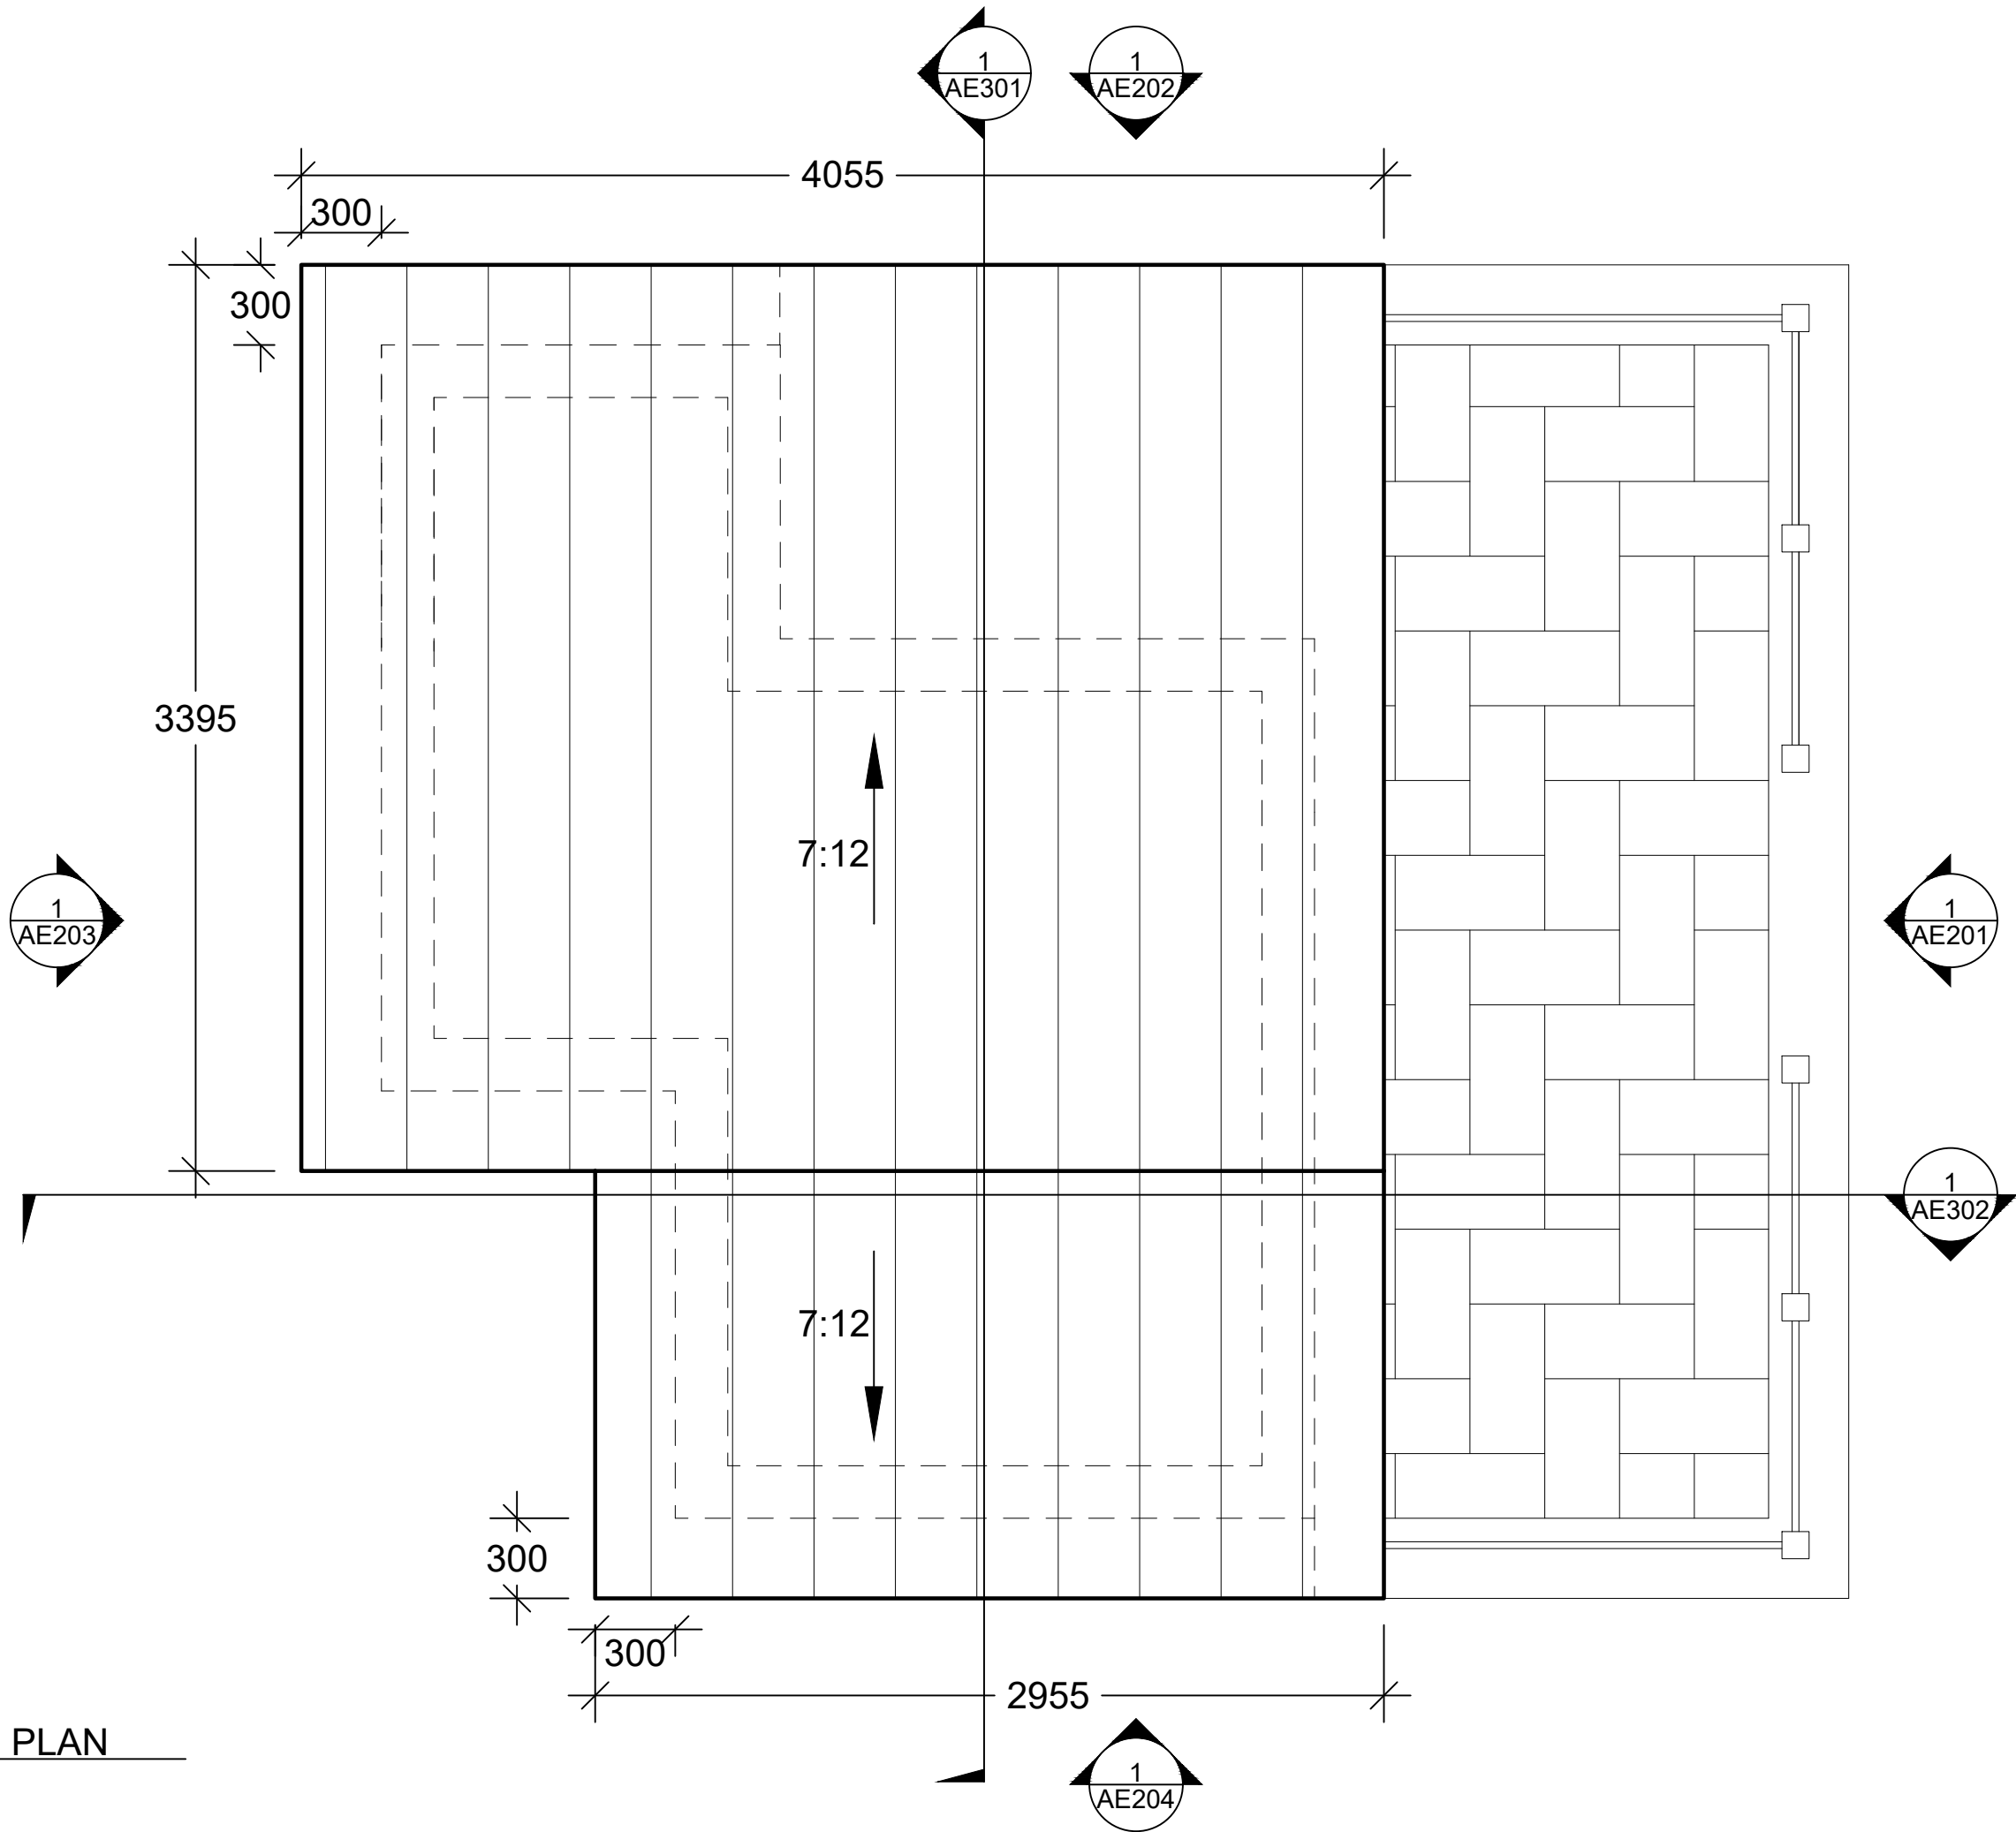

TINY RETREAT
PROJECT

ROOF PLAN


12/05/2025


mm

GROUP 8

1:25


AE103

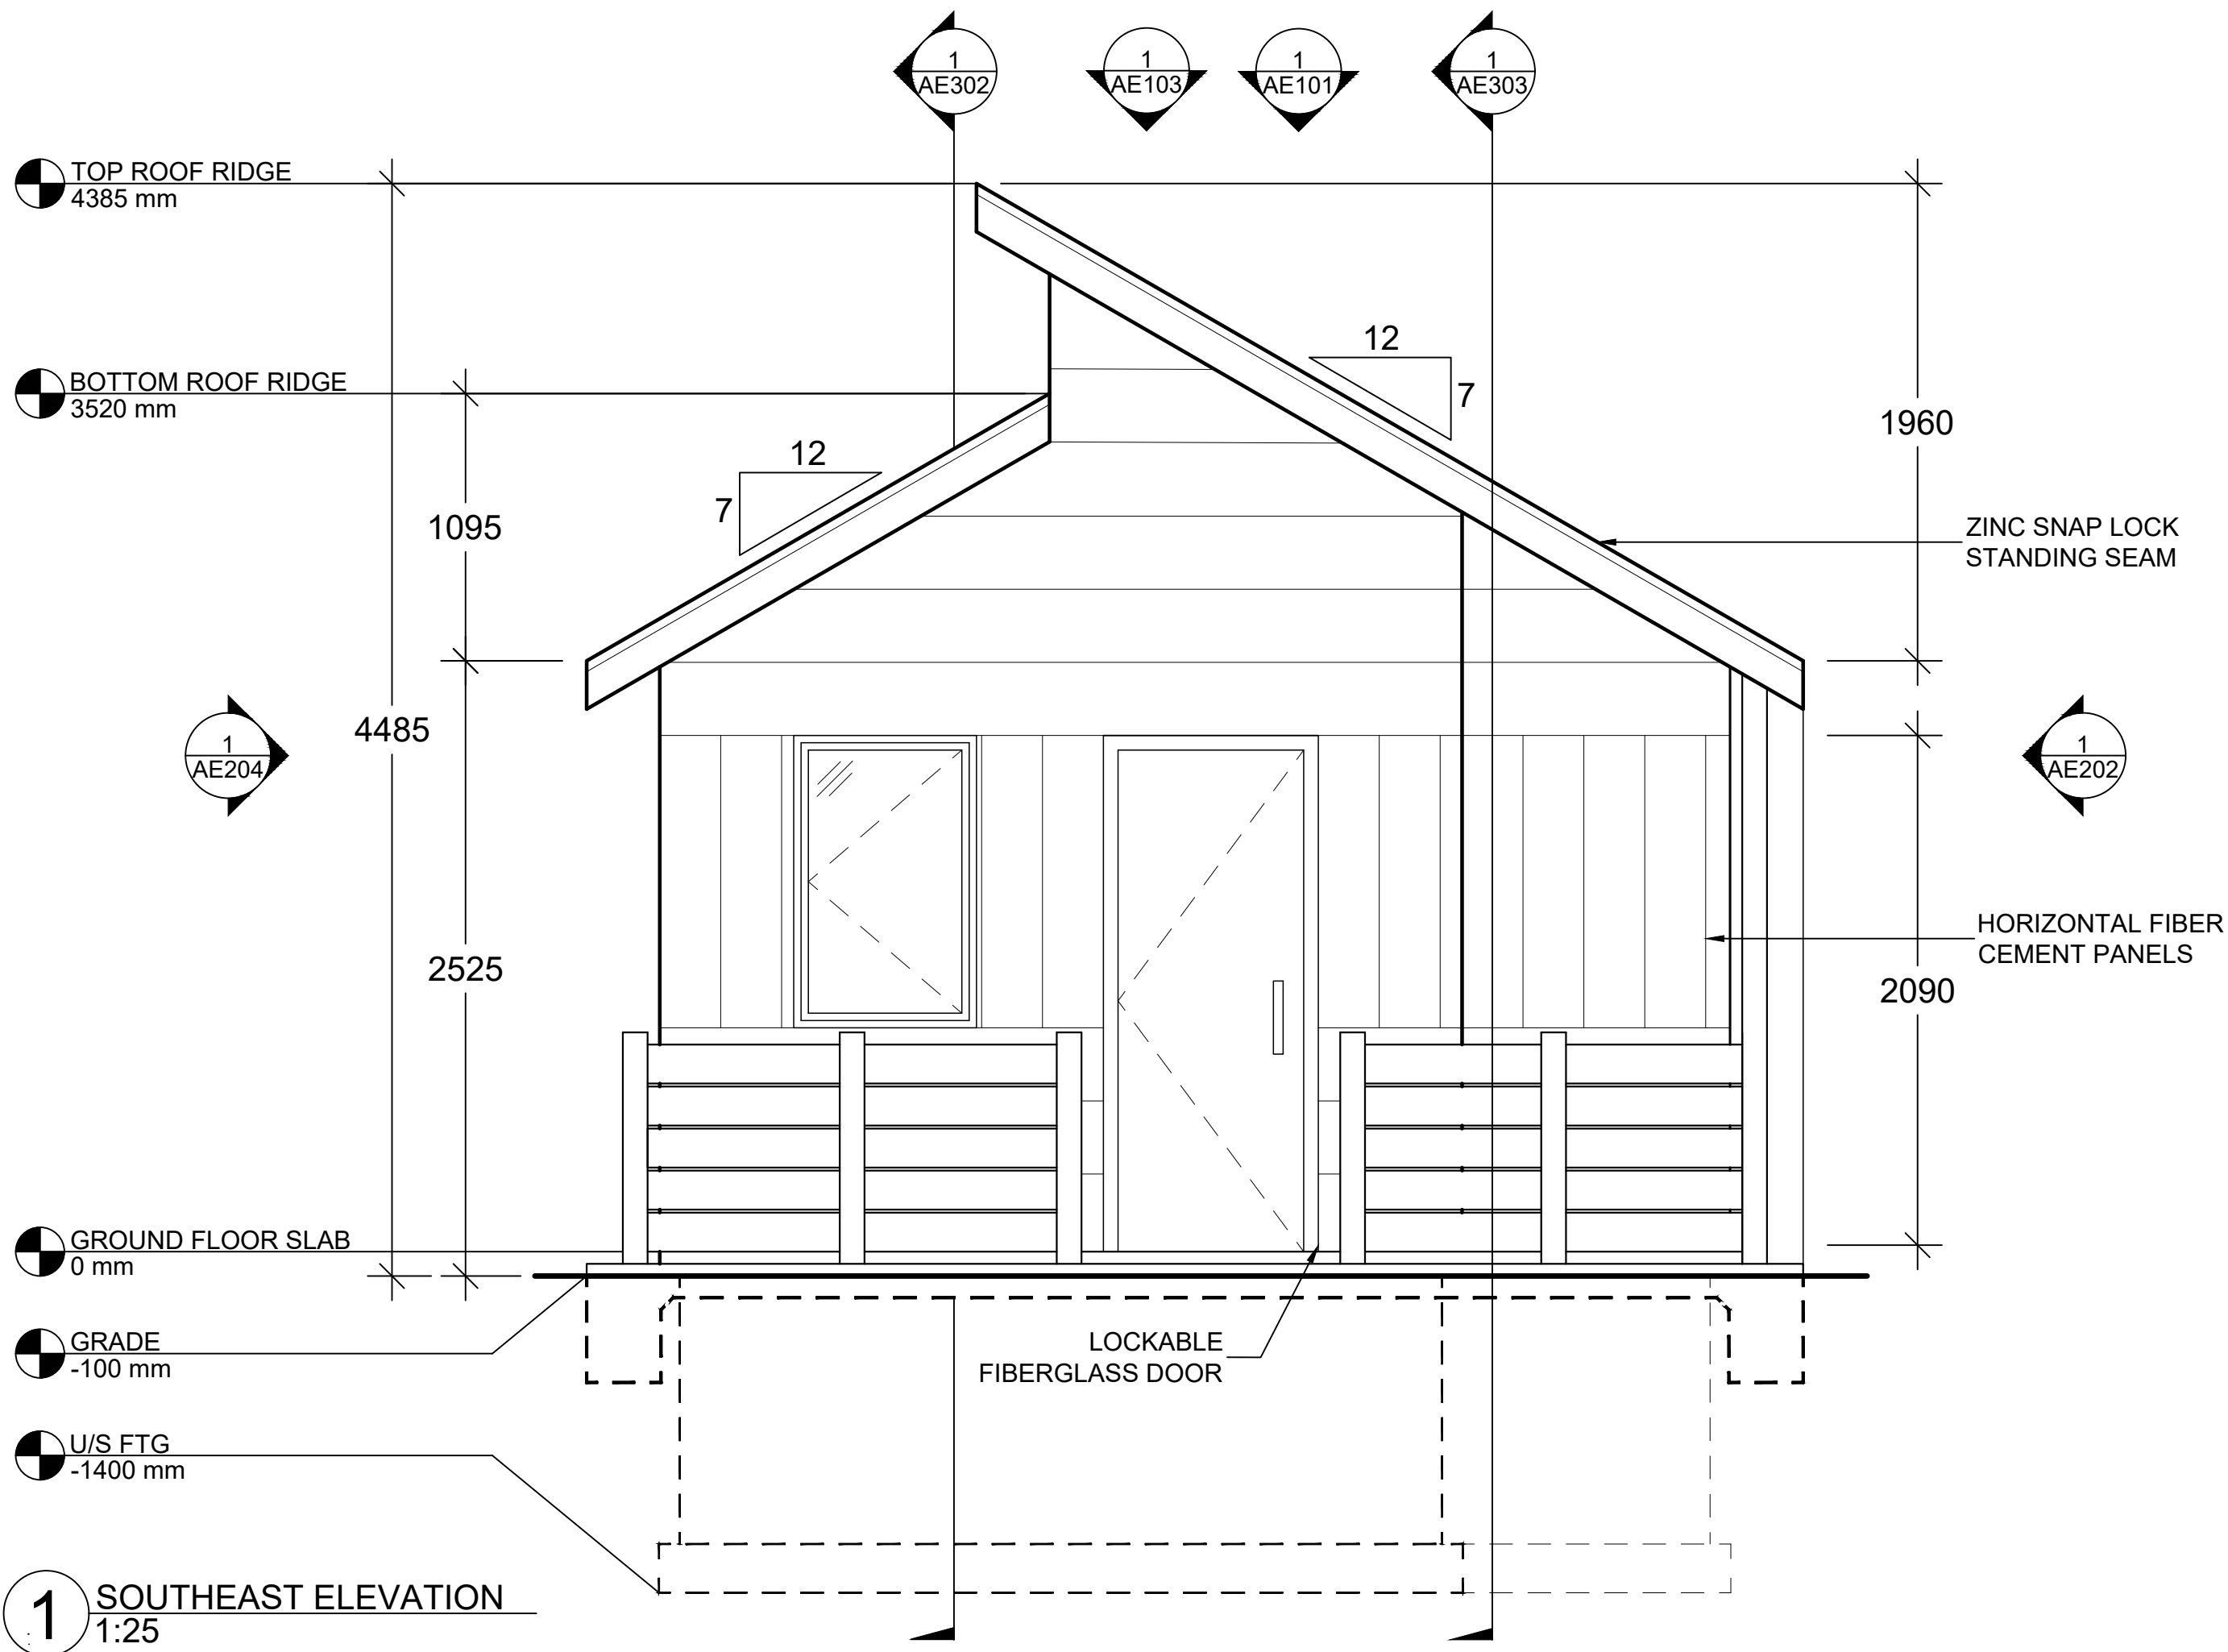

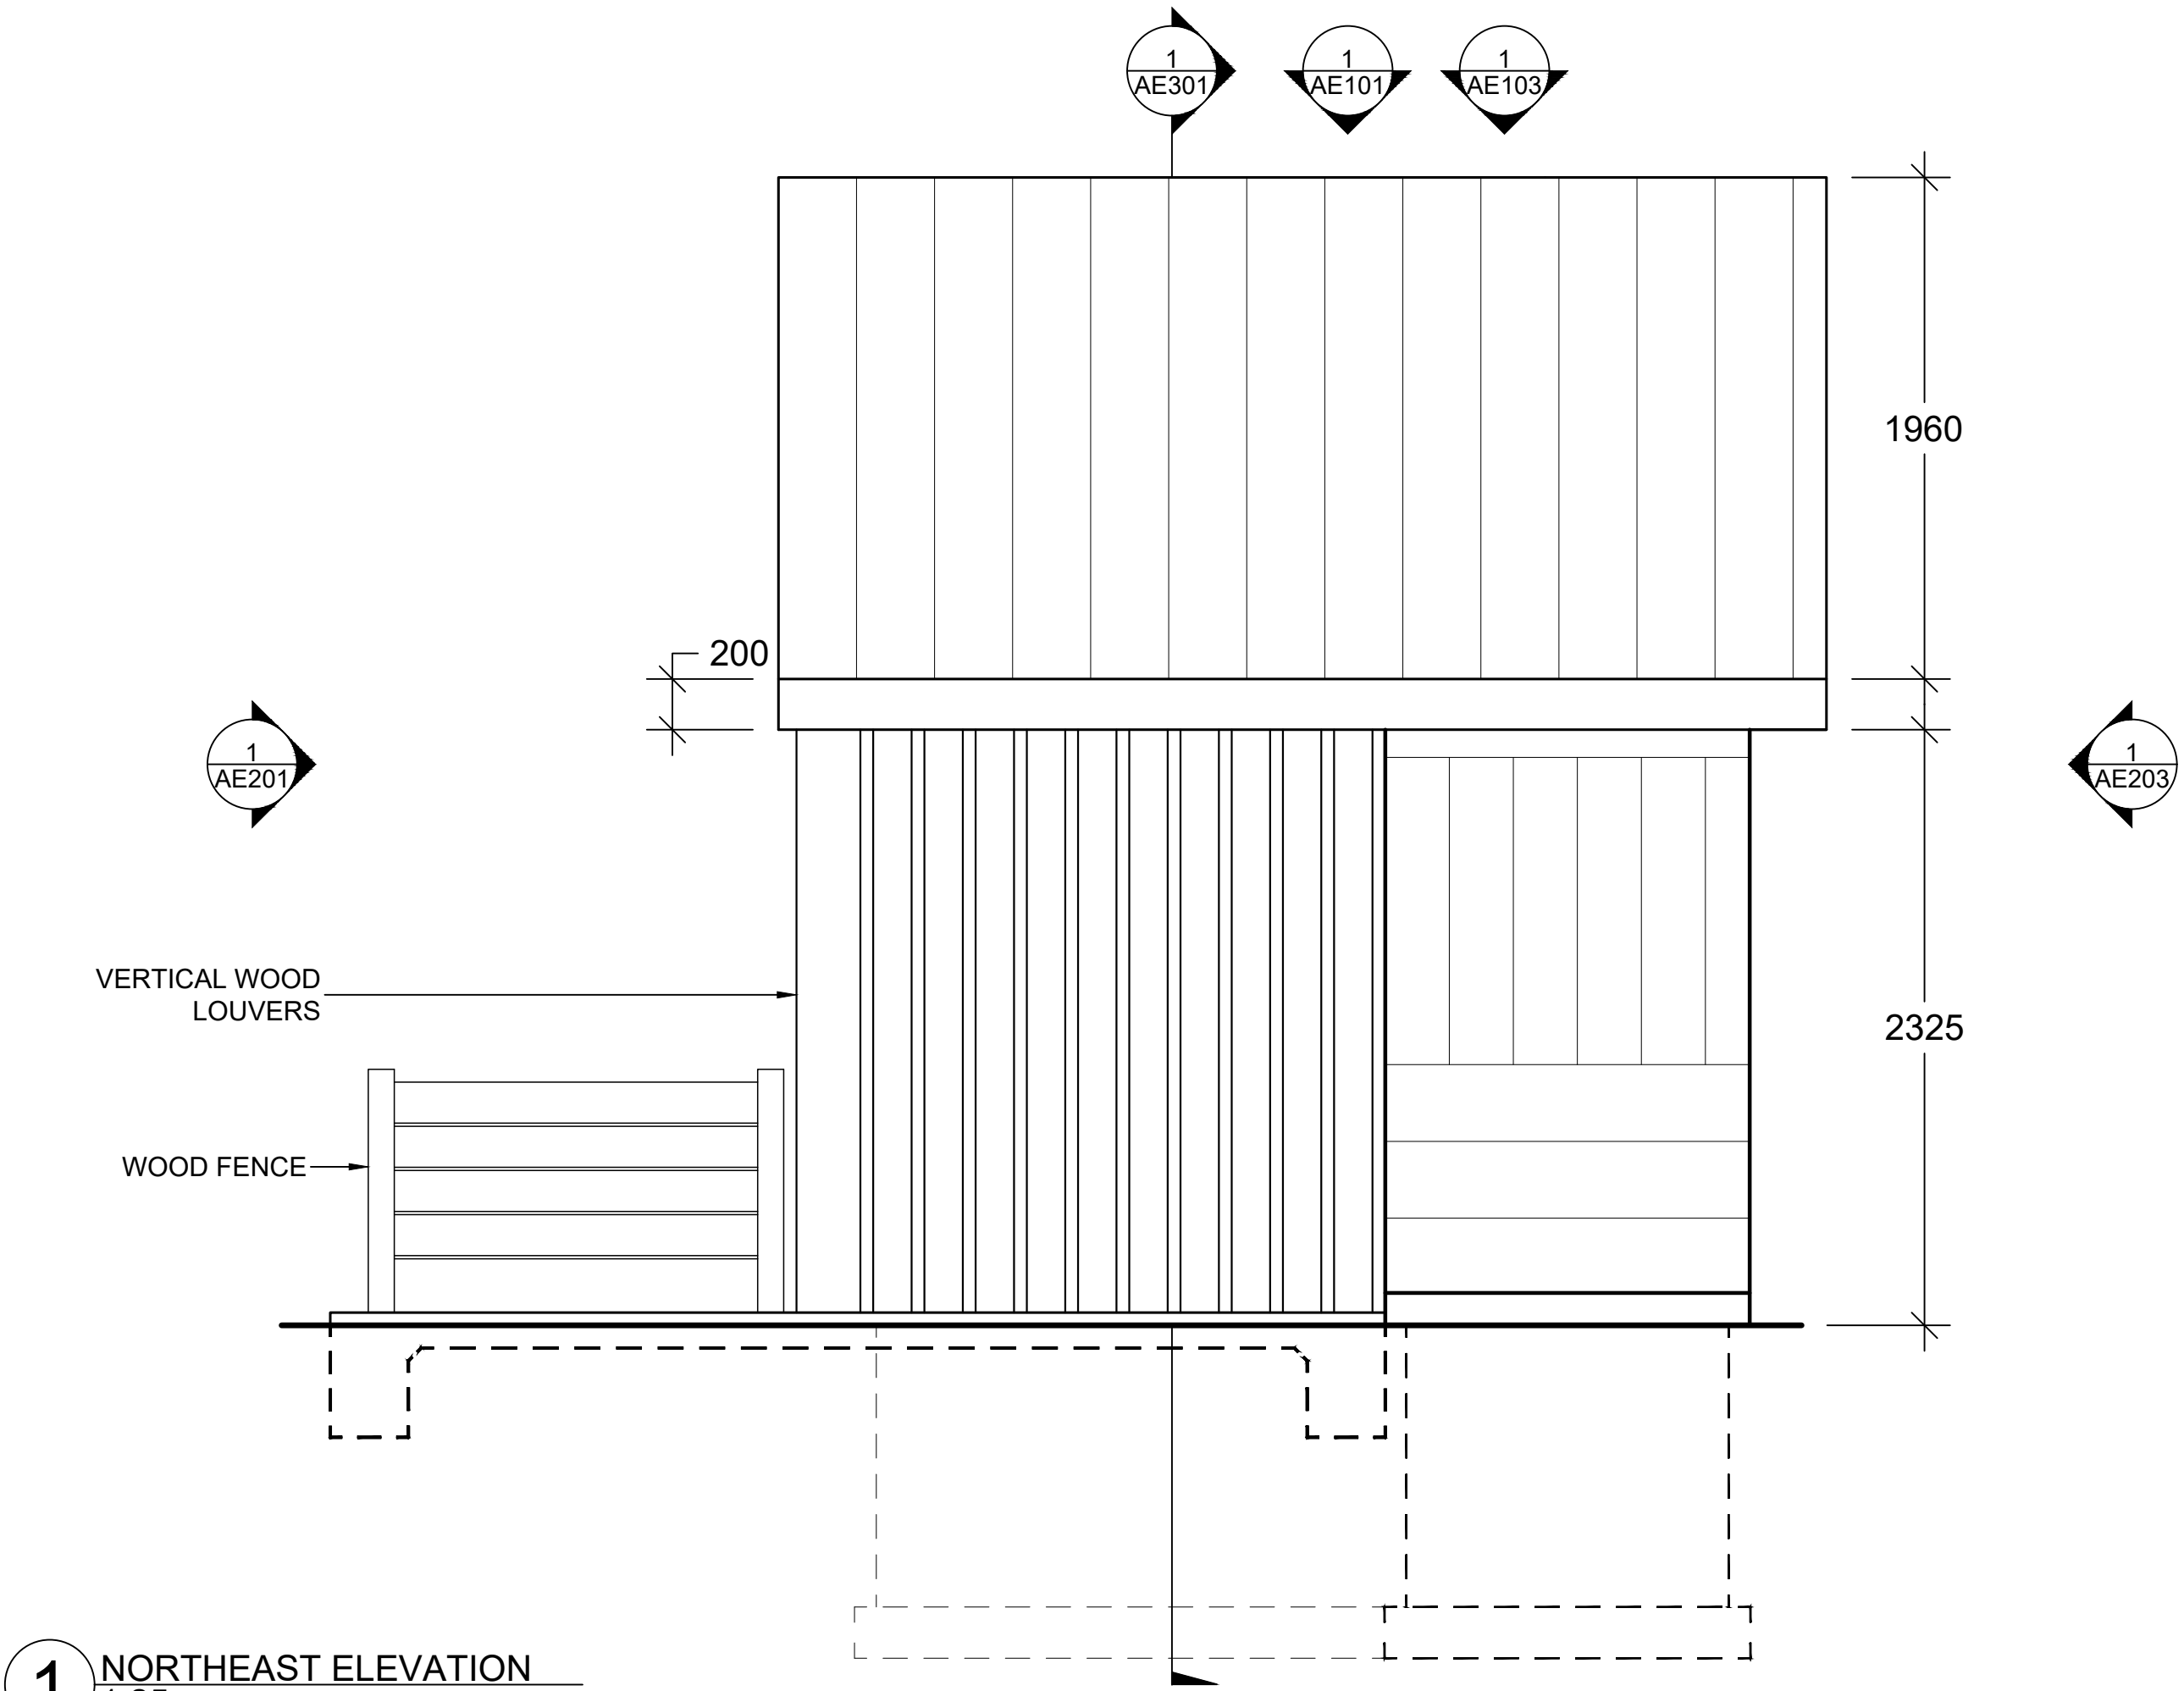

	
190 Westmount Rd N, Waterloo, ON N2L 3G5	
	
TINY RETREAT PROJECT	
NORTHEAST ELEVATION	
12/05/2025	mm
GROUP 8	AE202
1:25	

1 NORTHWEST ELEVATION
1:25

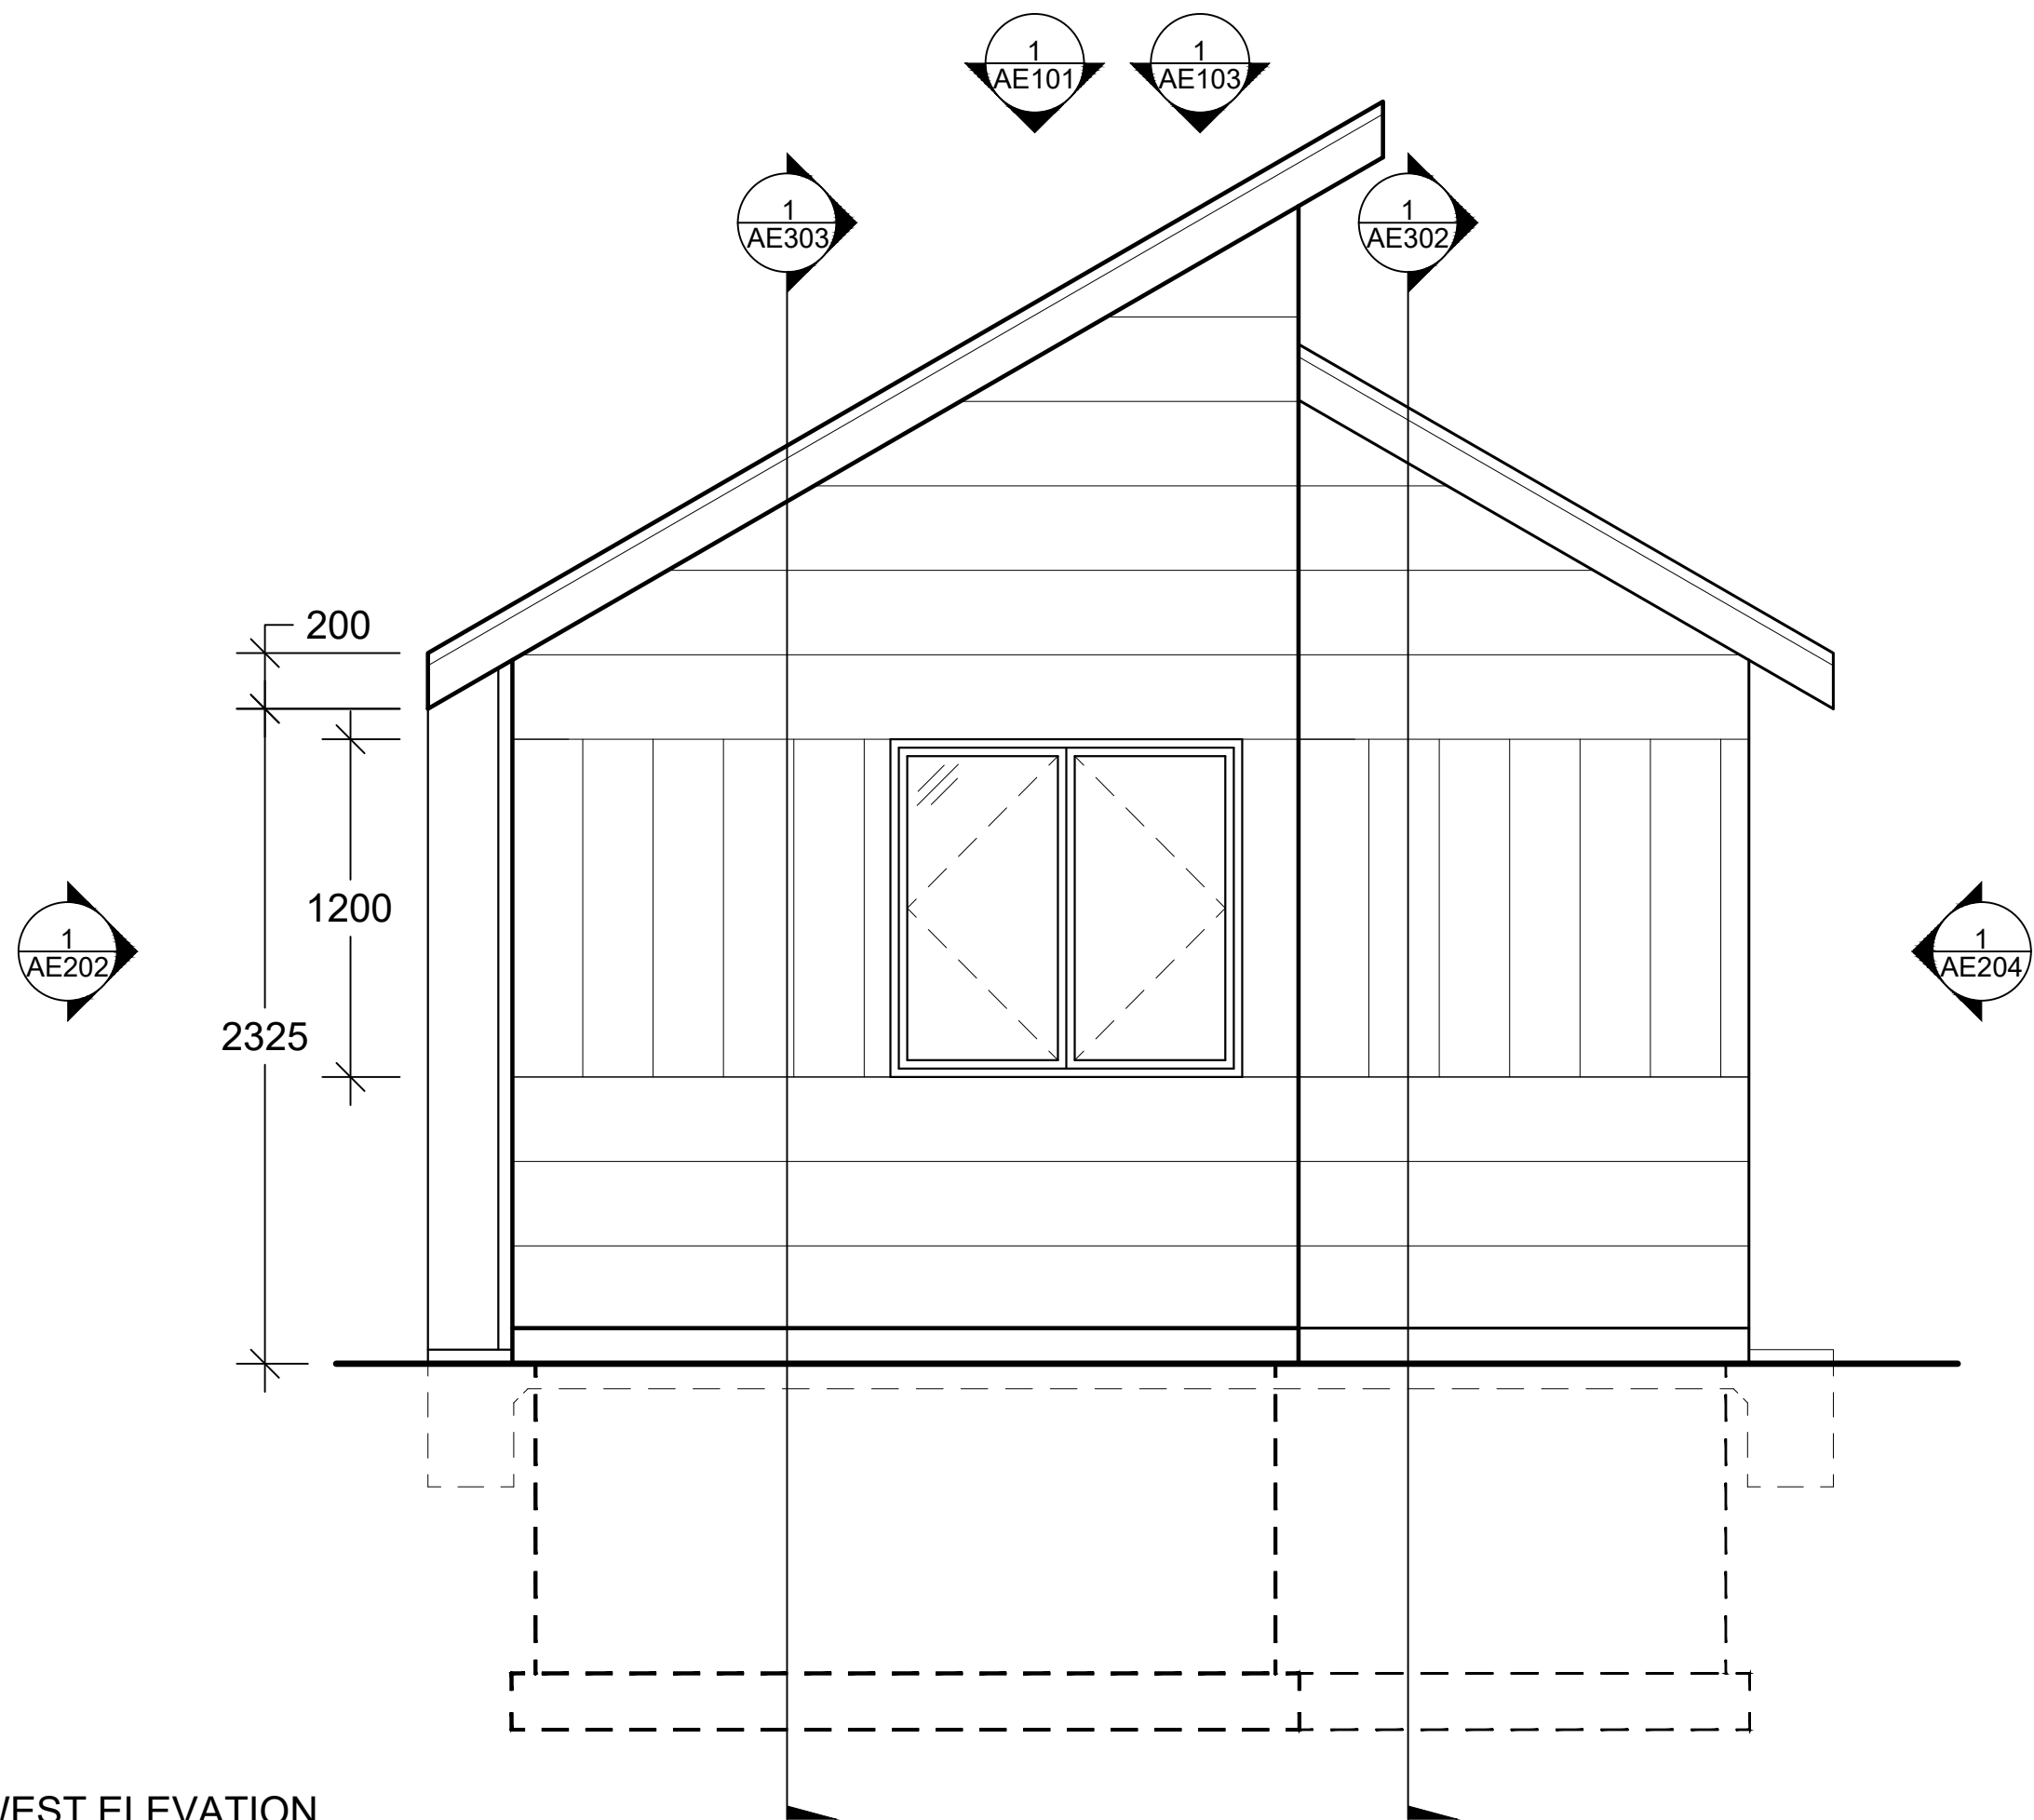

TINY RETREAT
PROJECT

NORTHWEST
ELEVATION


12/05/2025

mm

GROUP 8

1:25

AE203

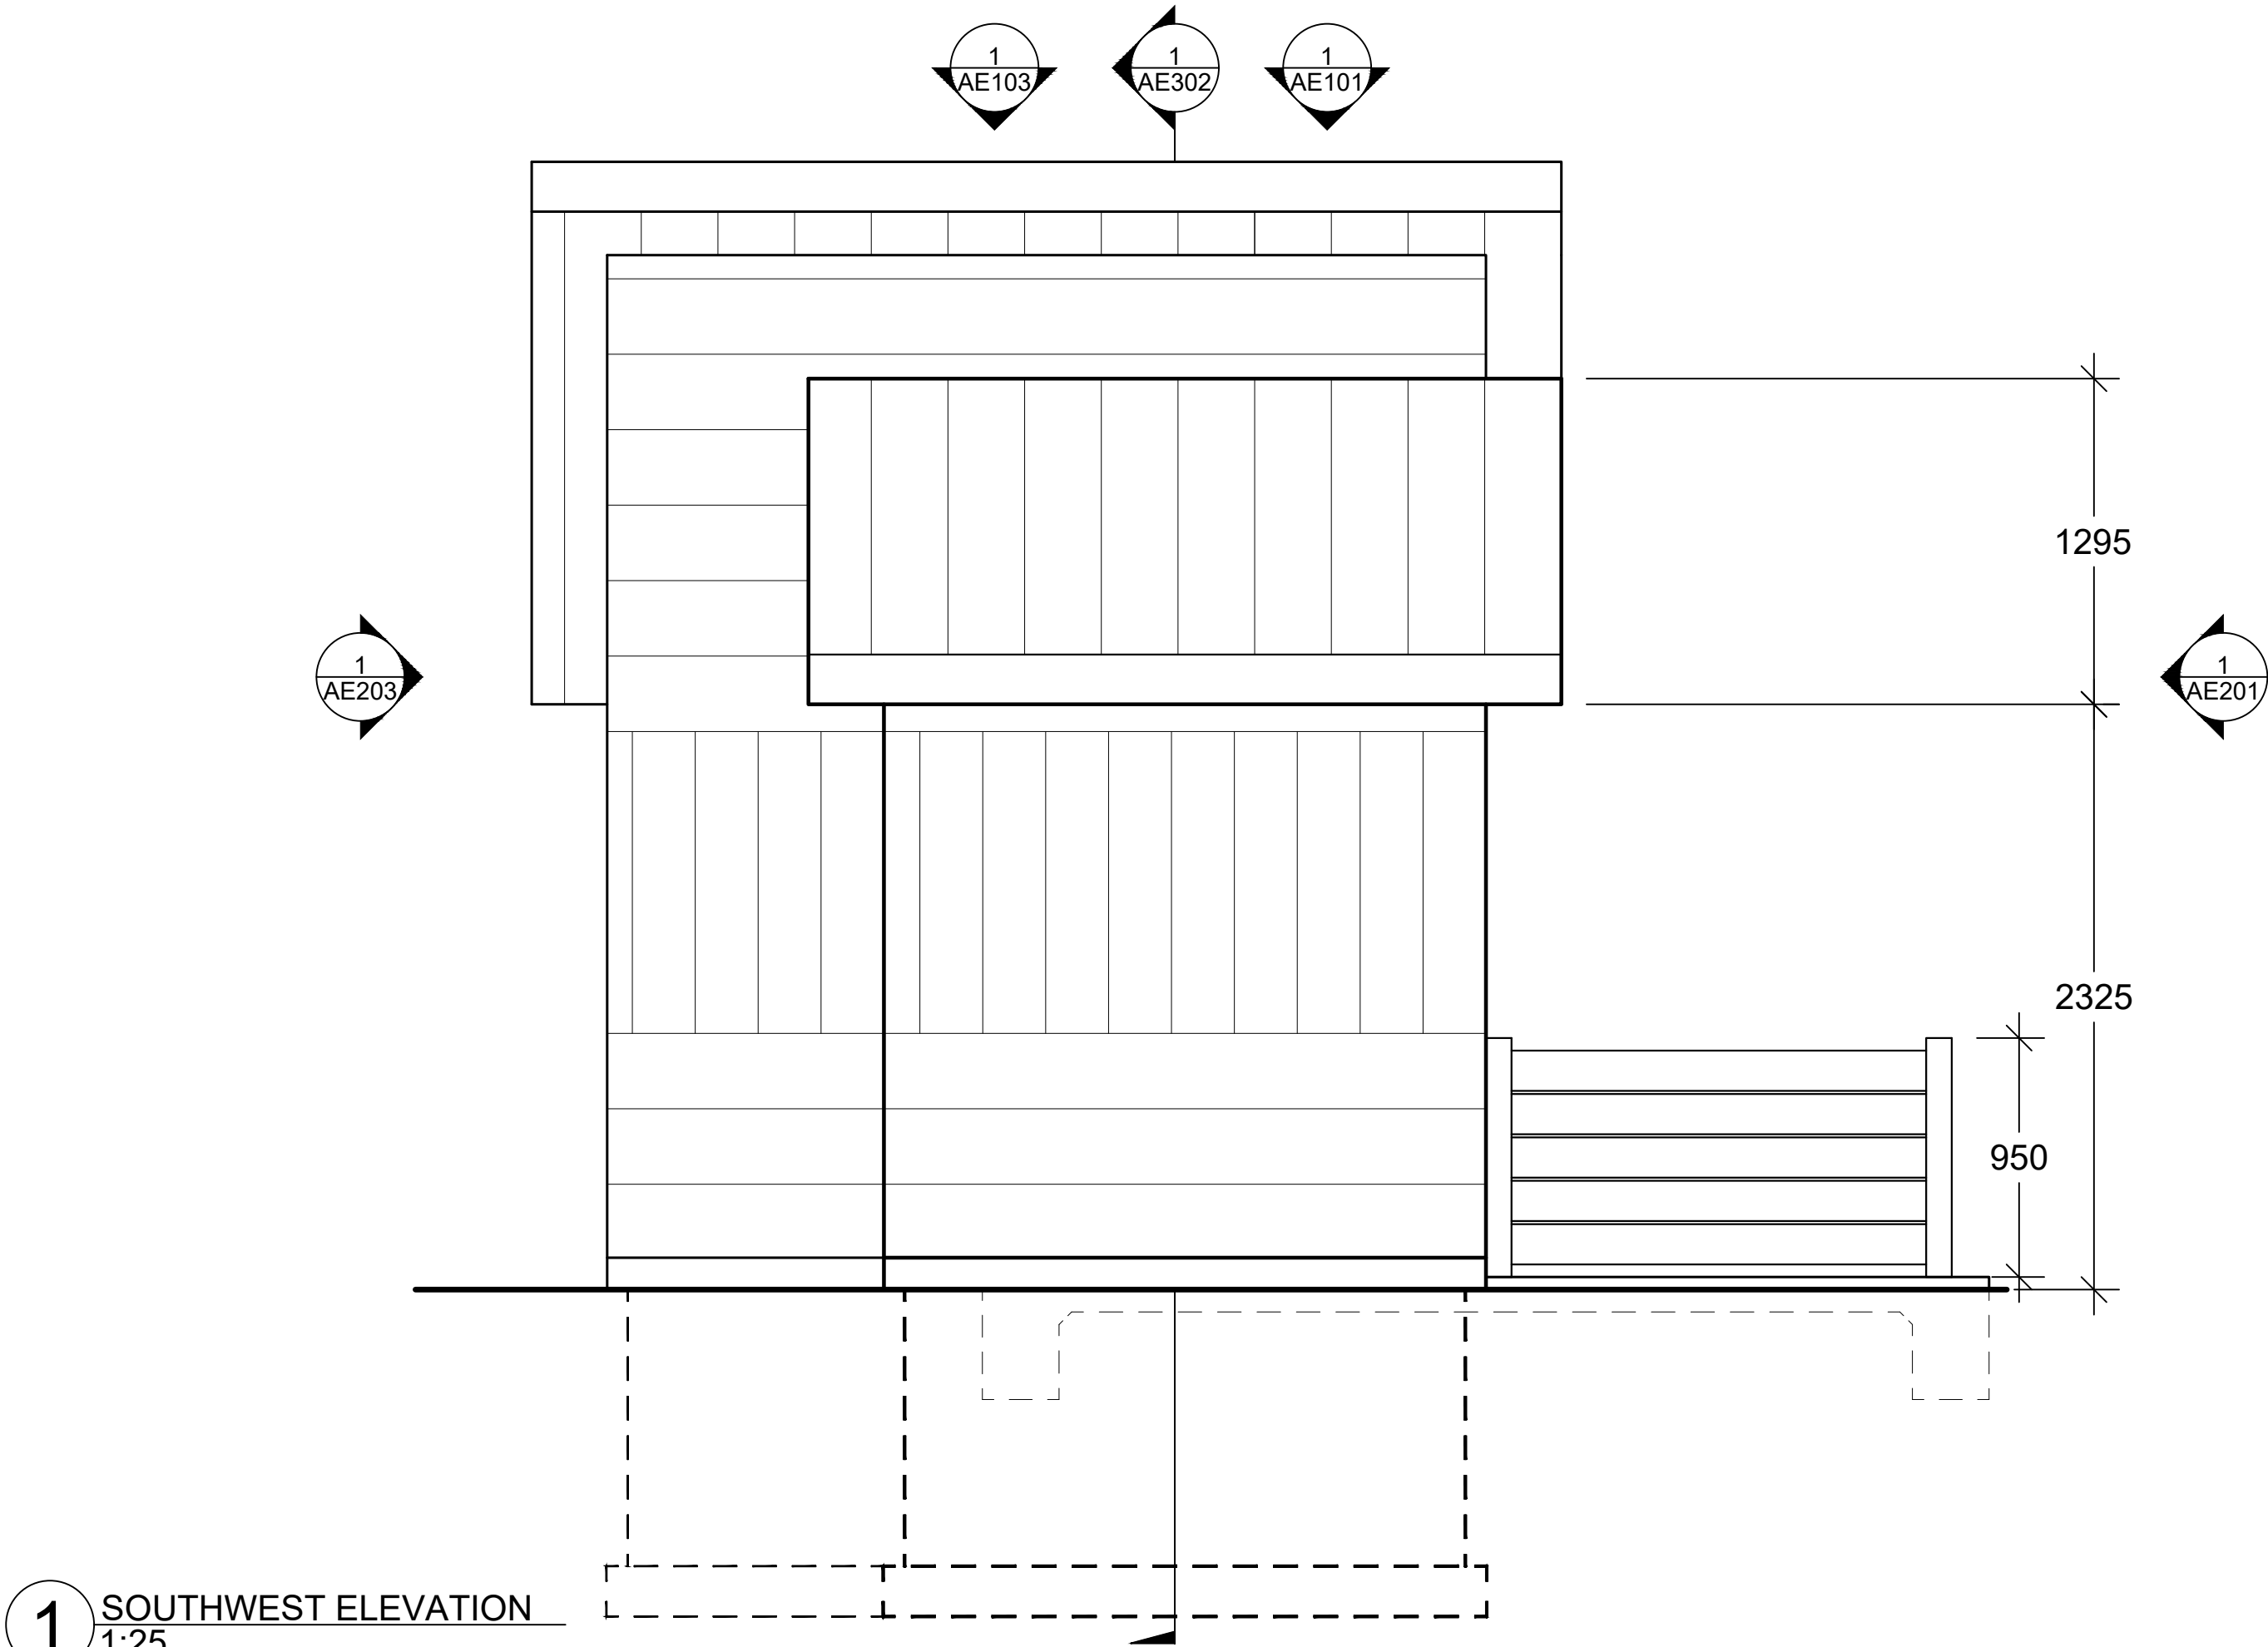

1 SOUTHWEST ELEVATION
1:25

	
190 Westmount Rd N, Waterloo, ON N2L 3G5	
	
TINY RETREAT PROJECT	
SOUTHWEST ELEVATION	
12/05/2025	mm
GROUP 8	AE204
1:25	



TINY RETREAT
PROJECT

SOUTHEAST
SECTION


12/05/2025

mm

GROUP 8

1:25

AE301

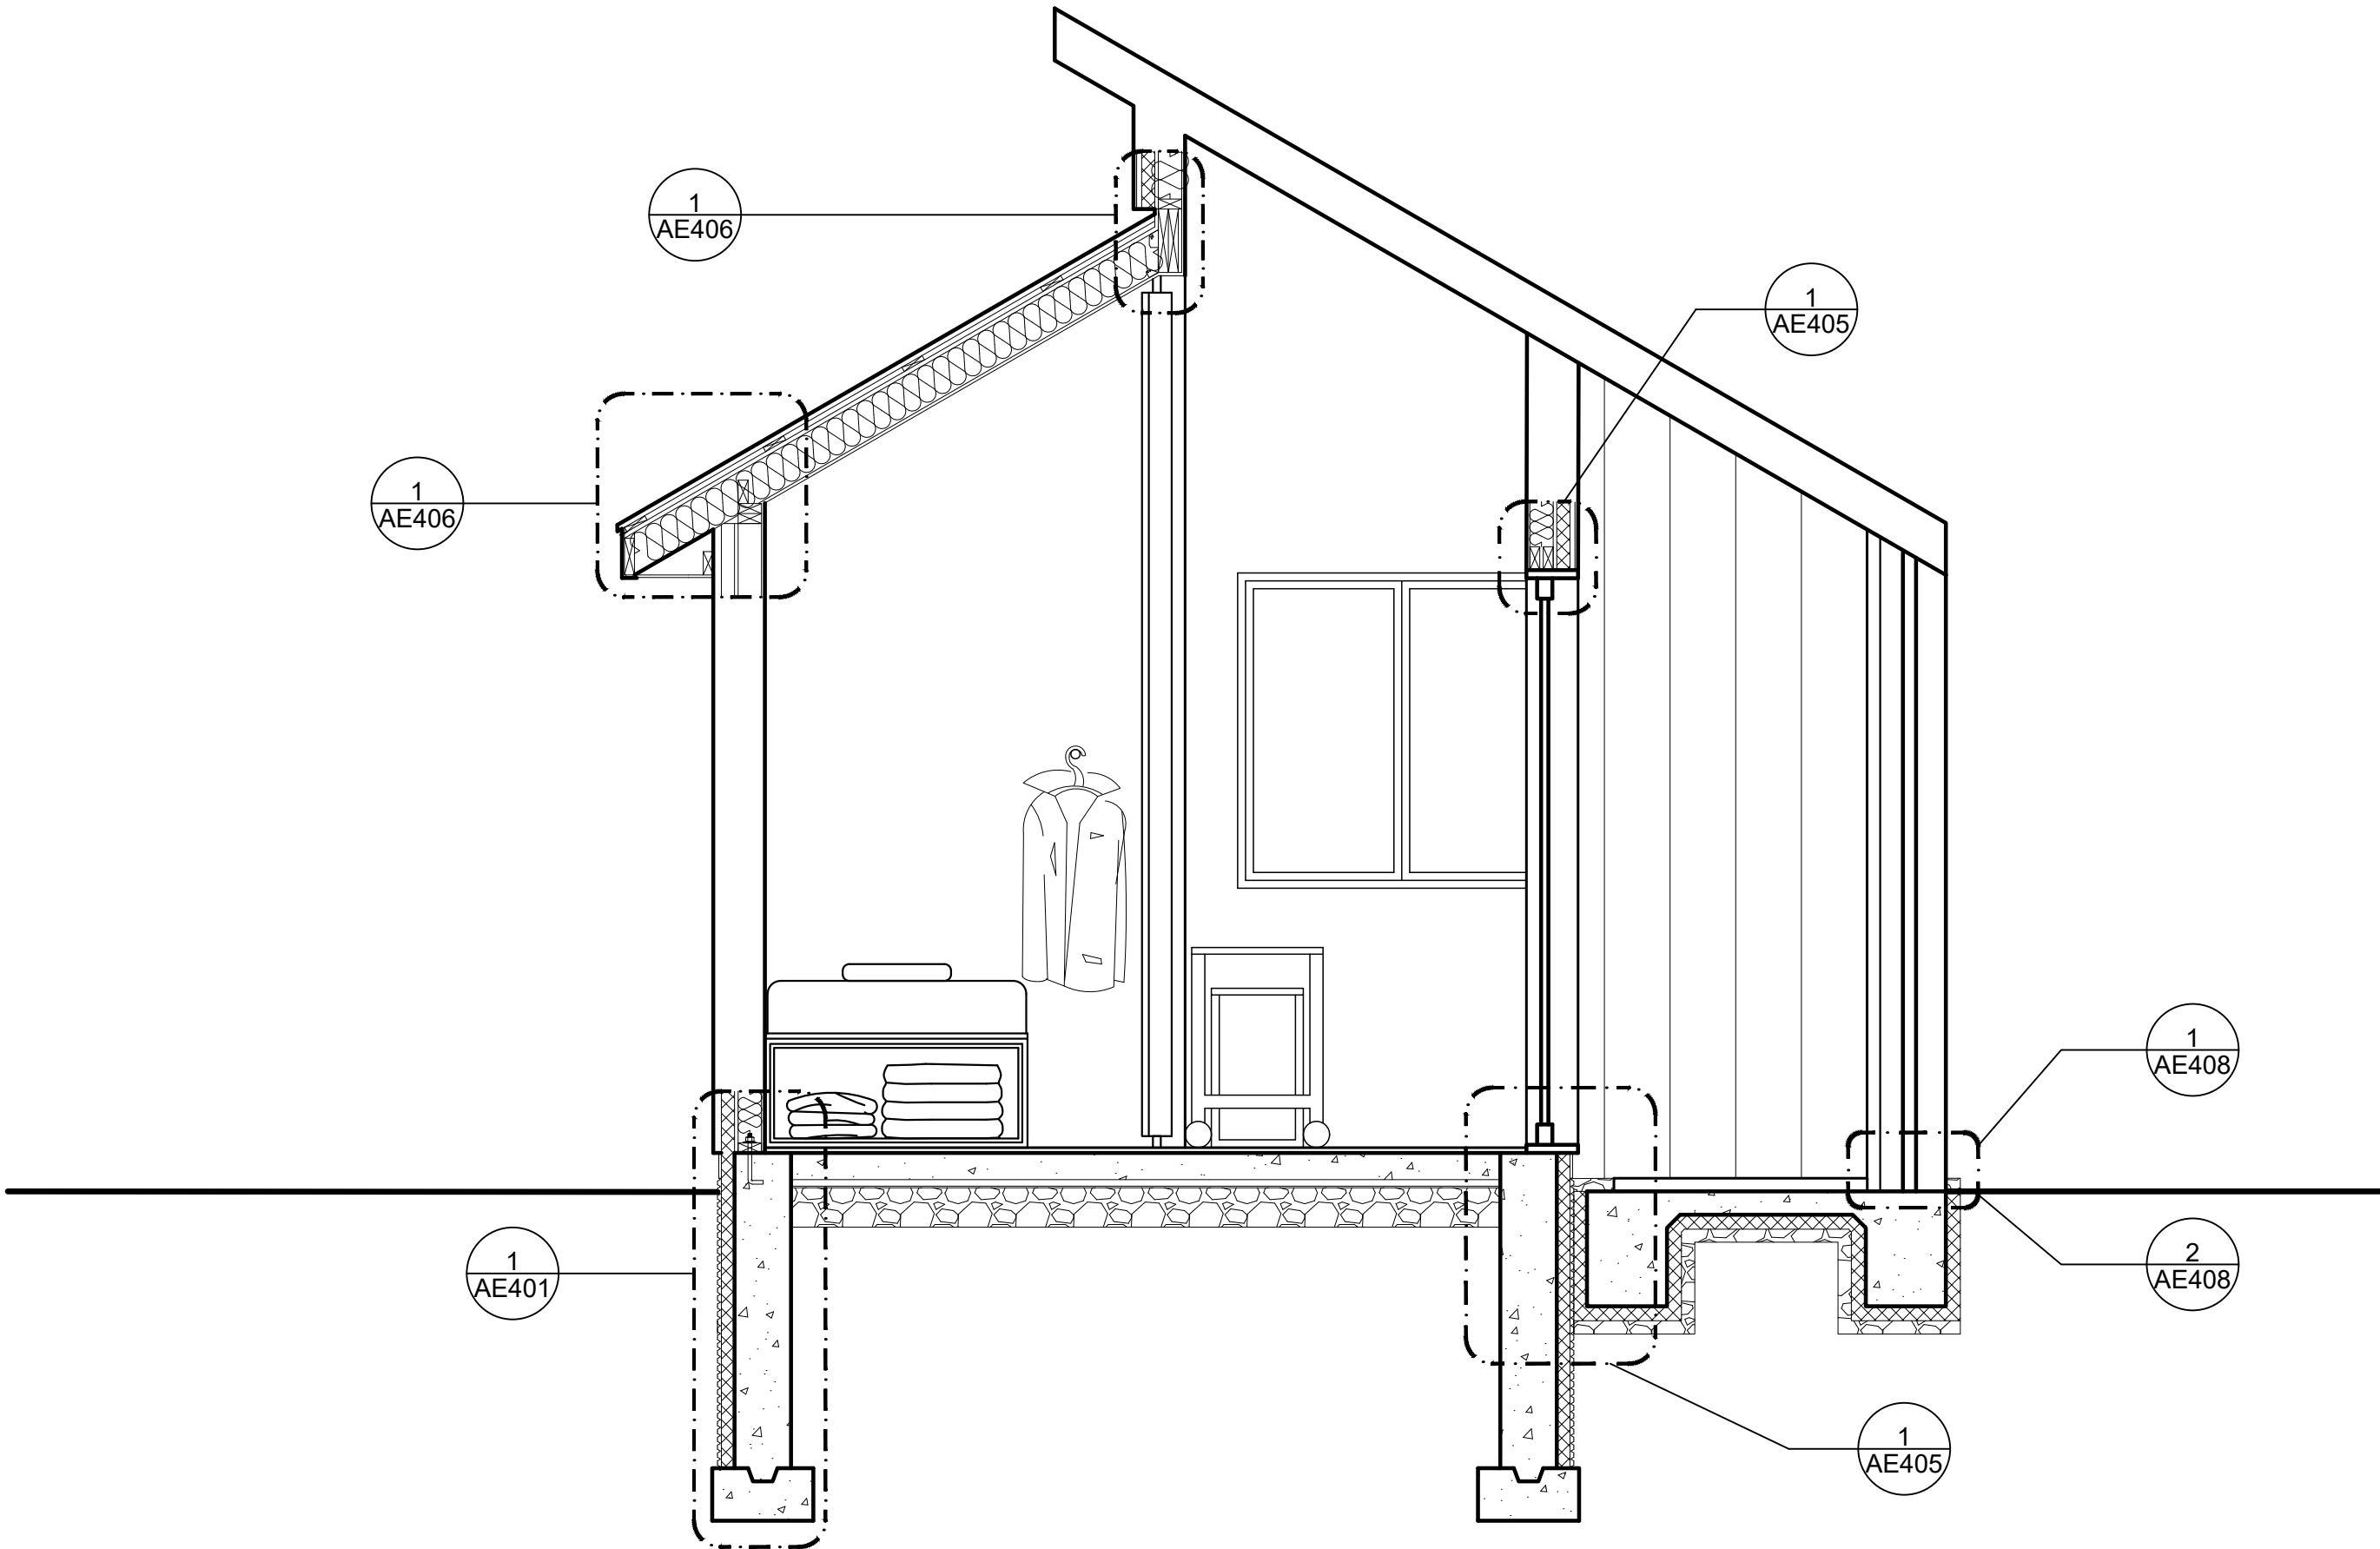


1

SOUTHEAST SECTION
1:25



190 Westmount Rd N,
Waterloo, ON N2L 3G5

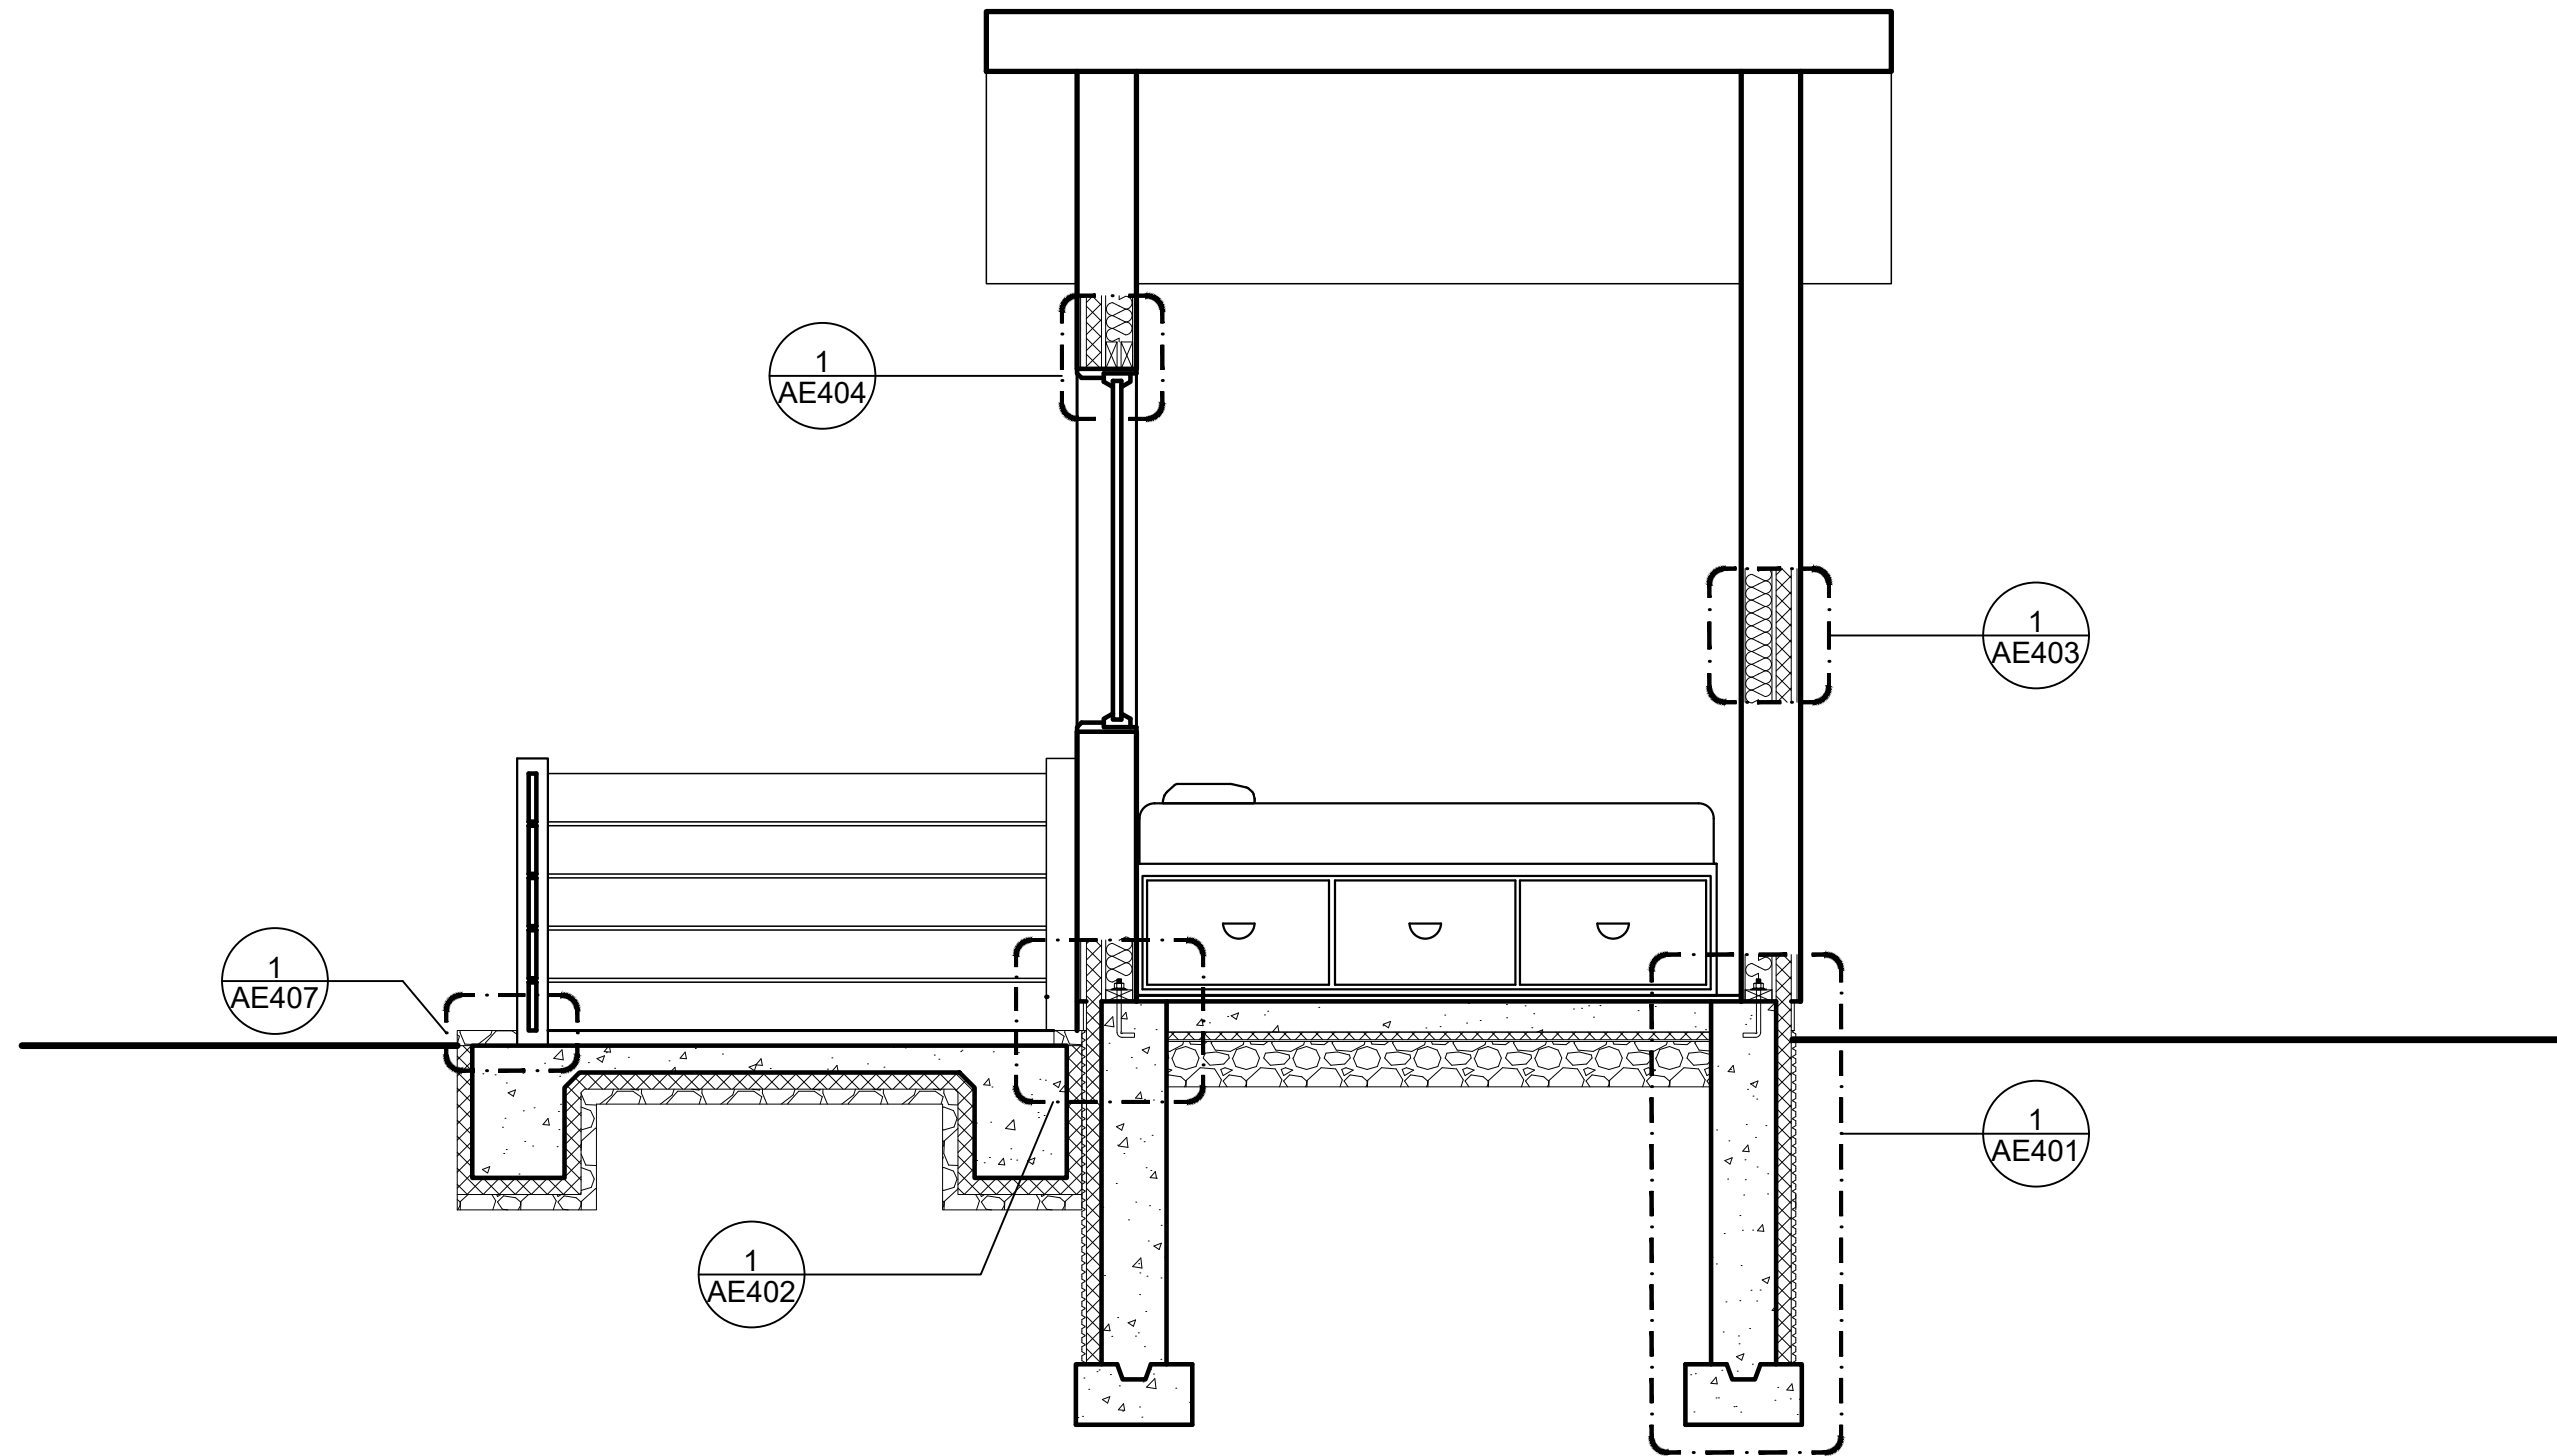

TINY RETREAT PROJECT

BED SECTION

12/05/2025

mm

GROUP 8

AE302

1:25

1 BED SECTION
1:25

1:25



TINY RETREAT
PROJECT

SLIDING DOOR
SECTION


12/05/2025

mm

GROUP 8

1:25

AE303

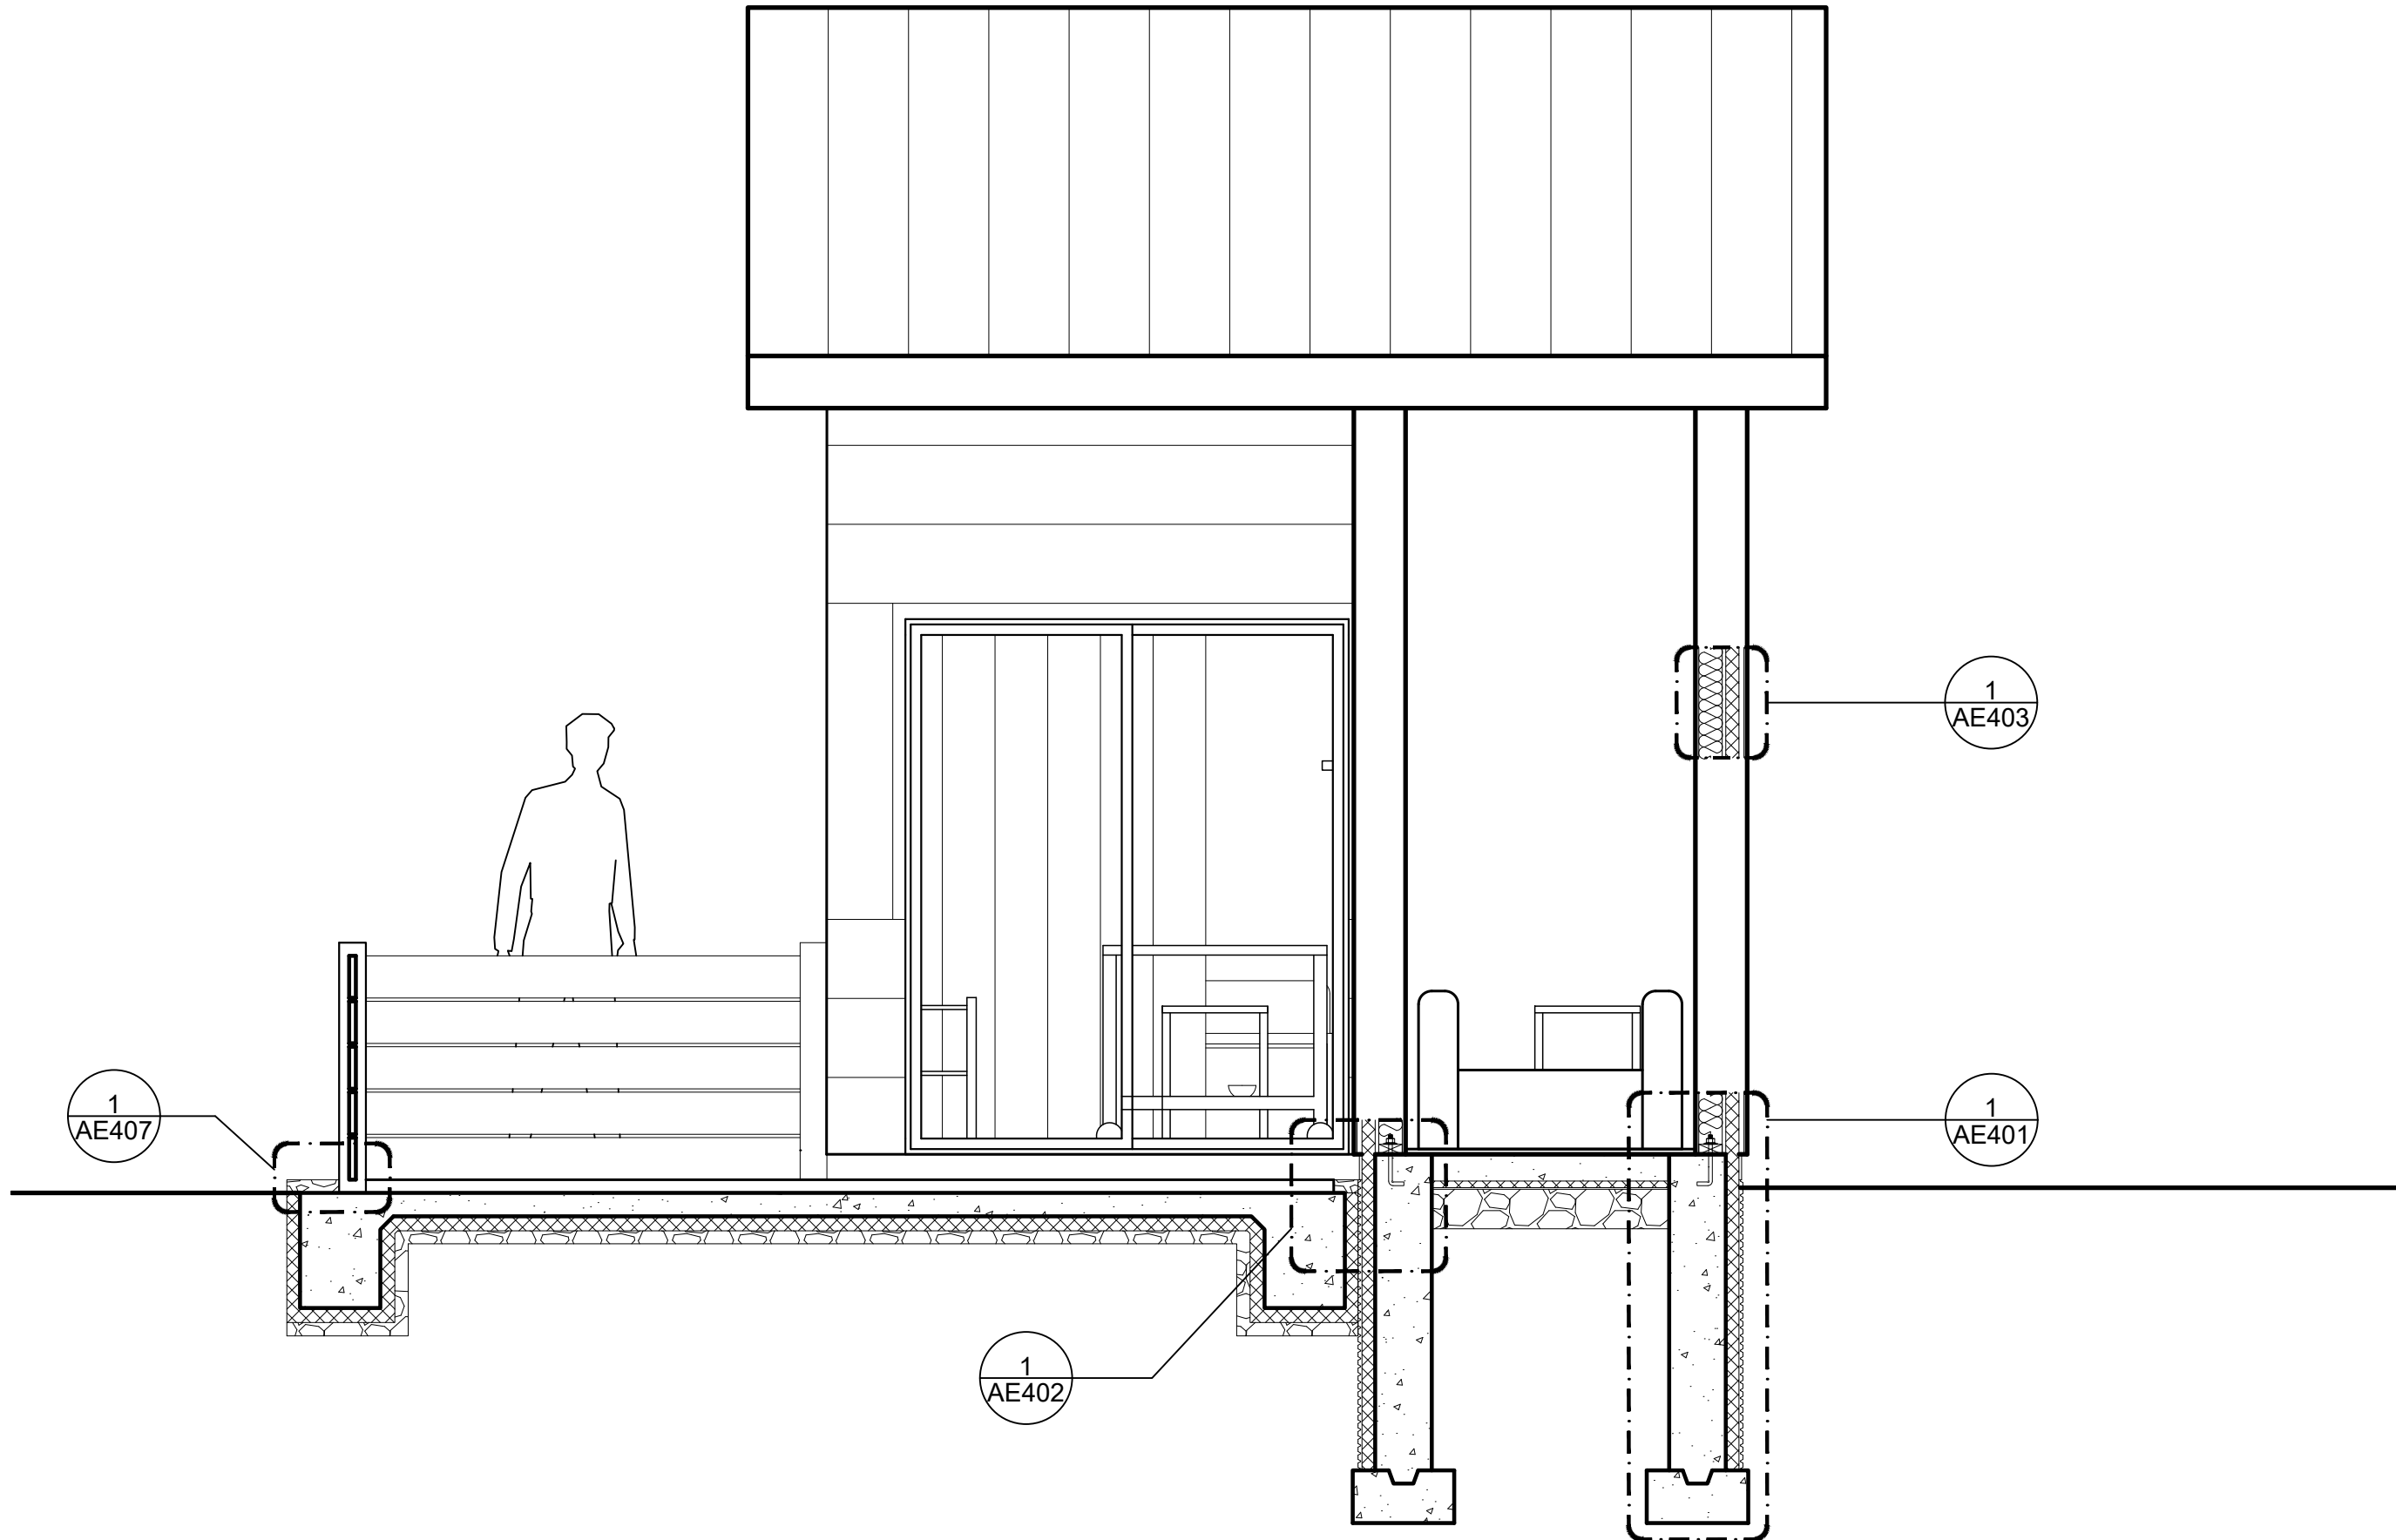

1

SLIDING DOOR SECTION
1:25



TINY RETREAT PROJECT

SPREAD FOOTING FOUNDATION TO WALL DETAIL


12/05/2025


mm


GROUP 8

1:5

AE401

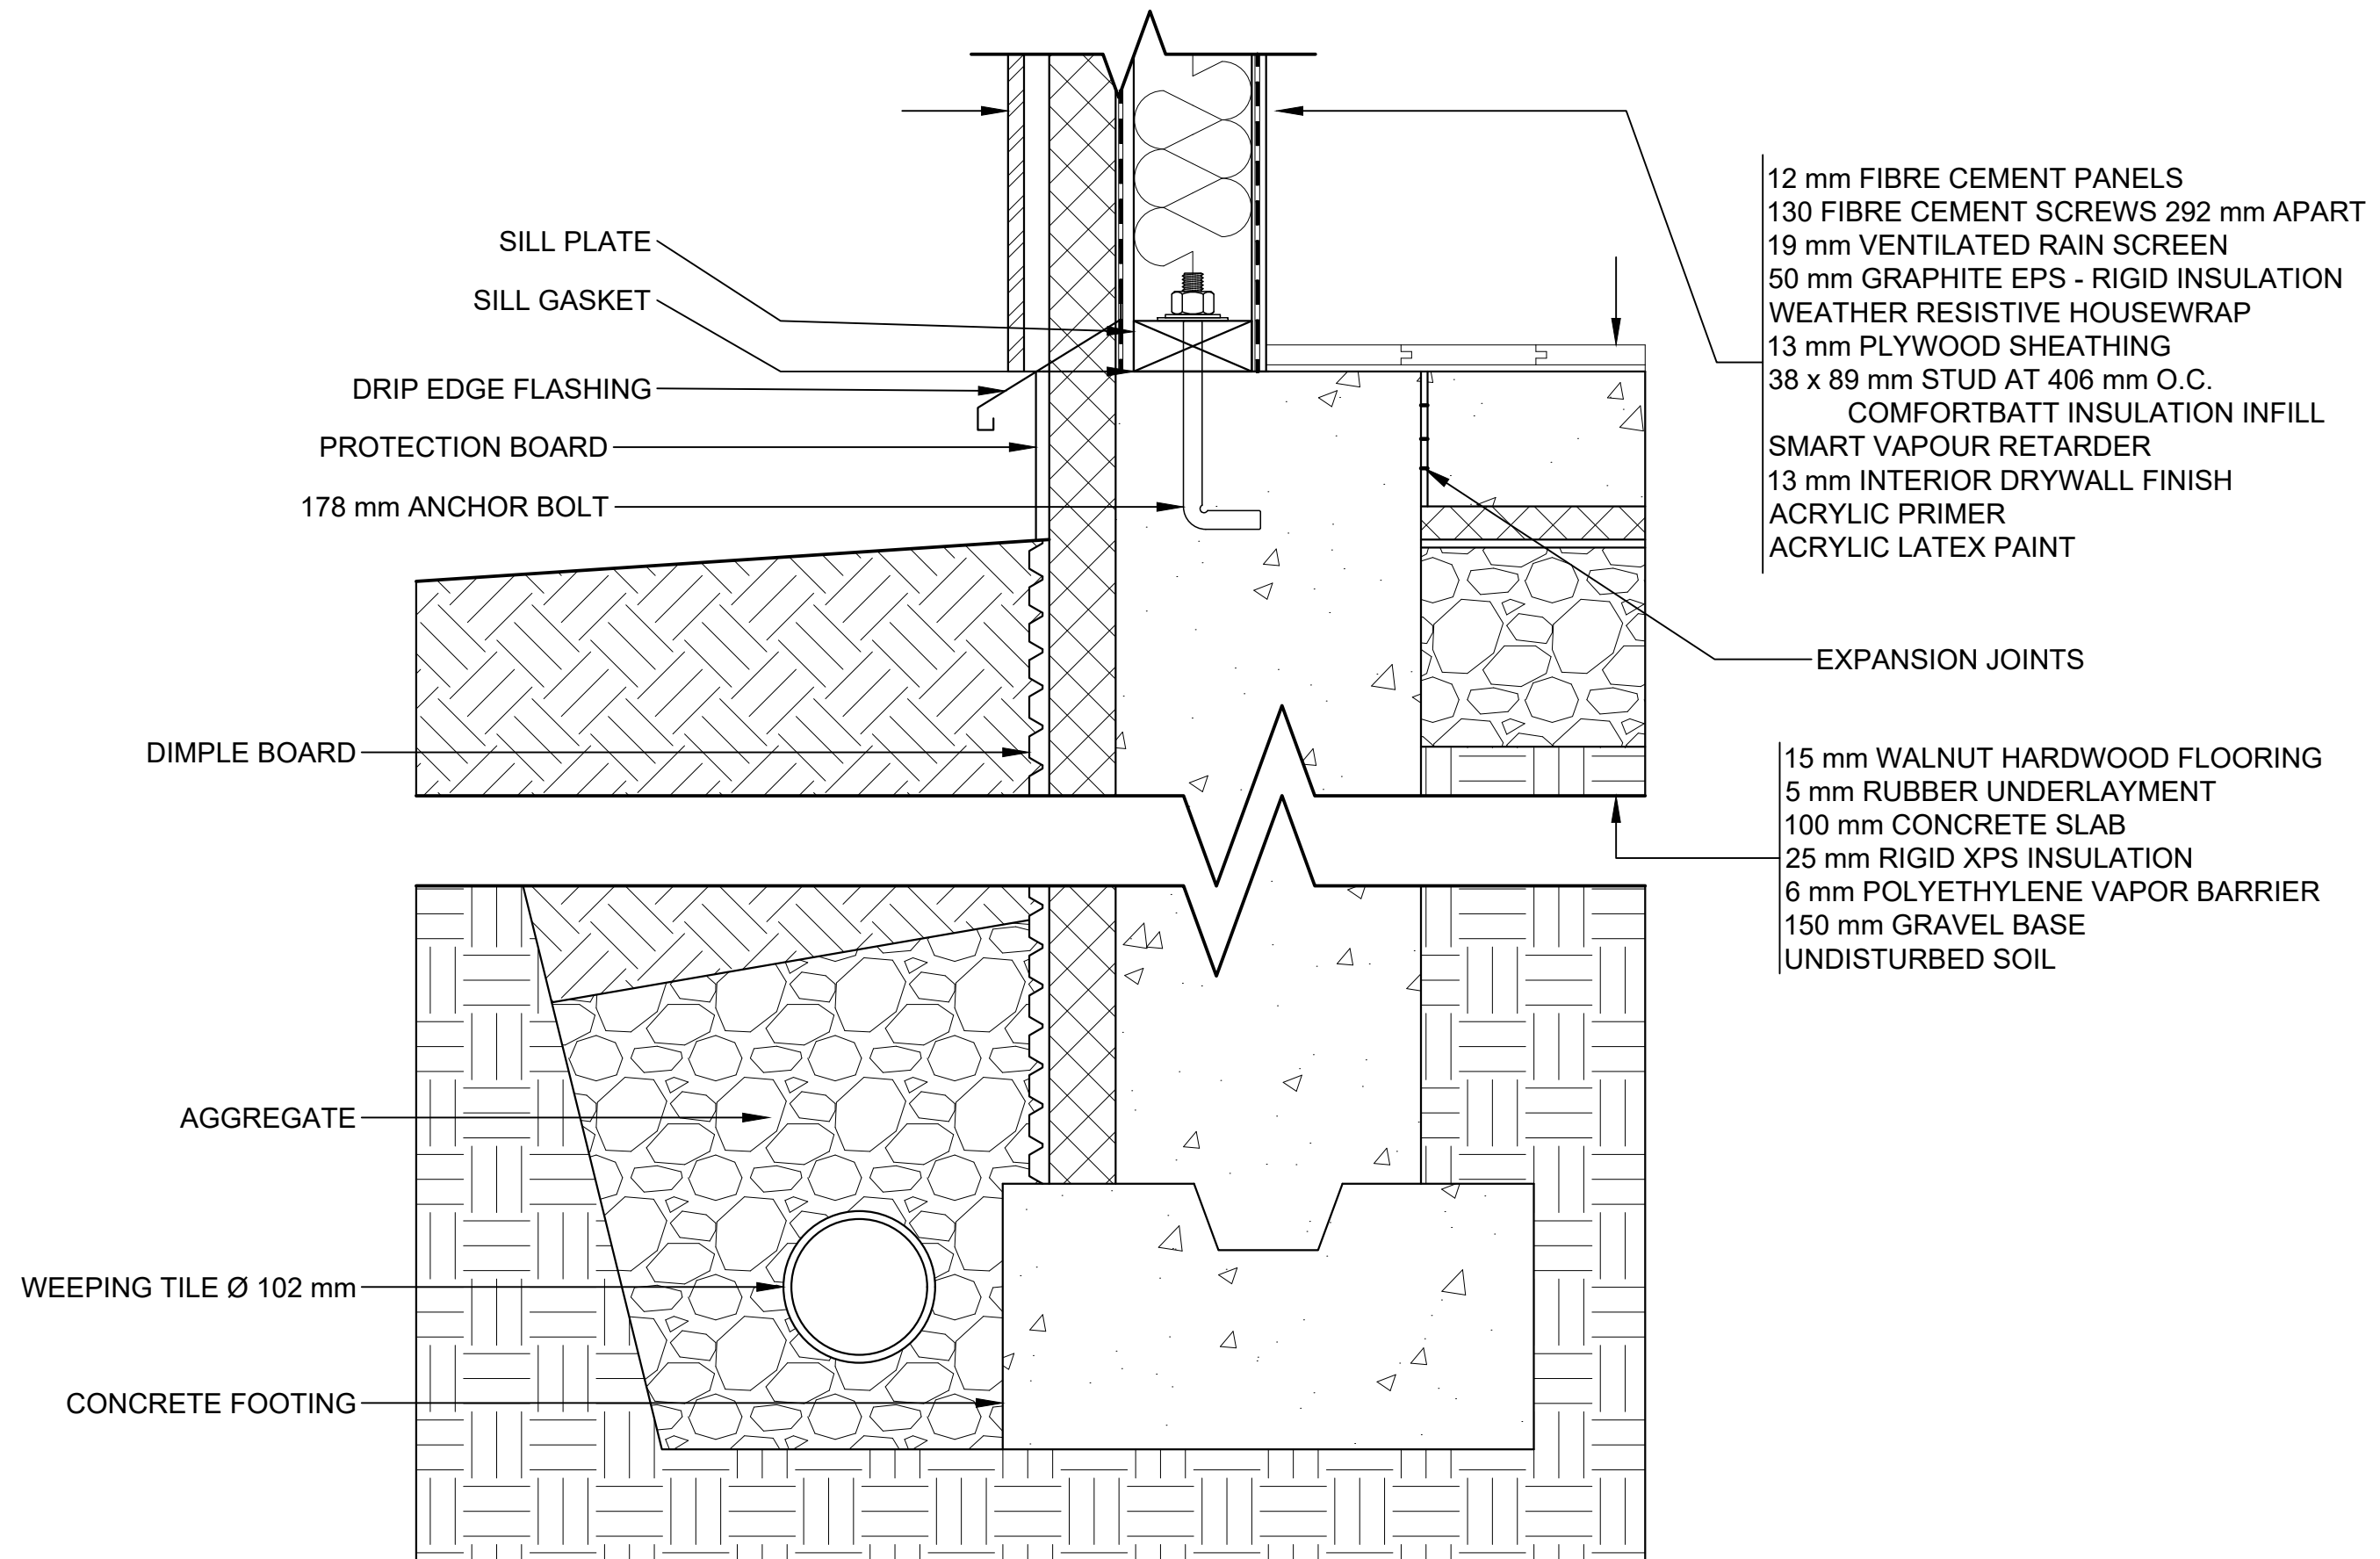

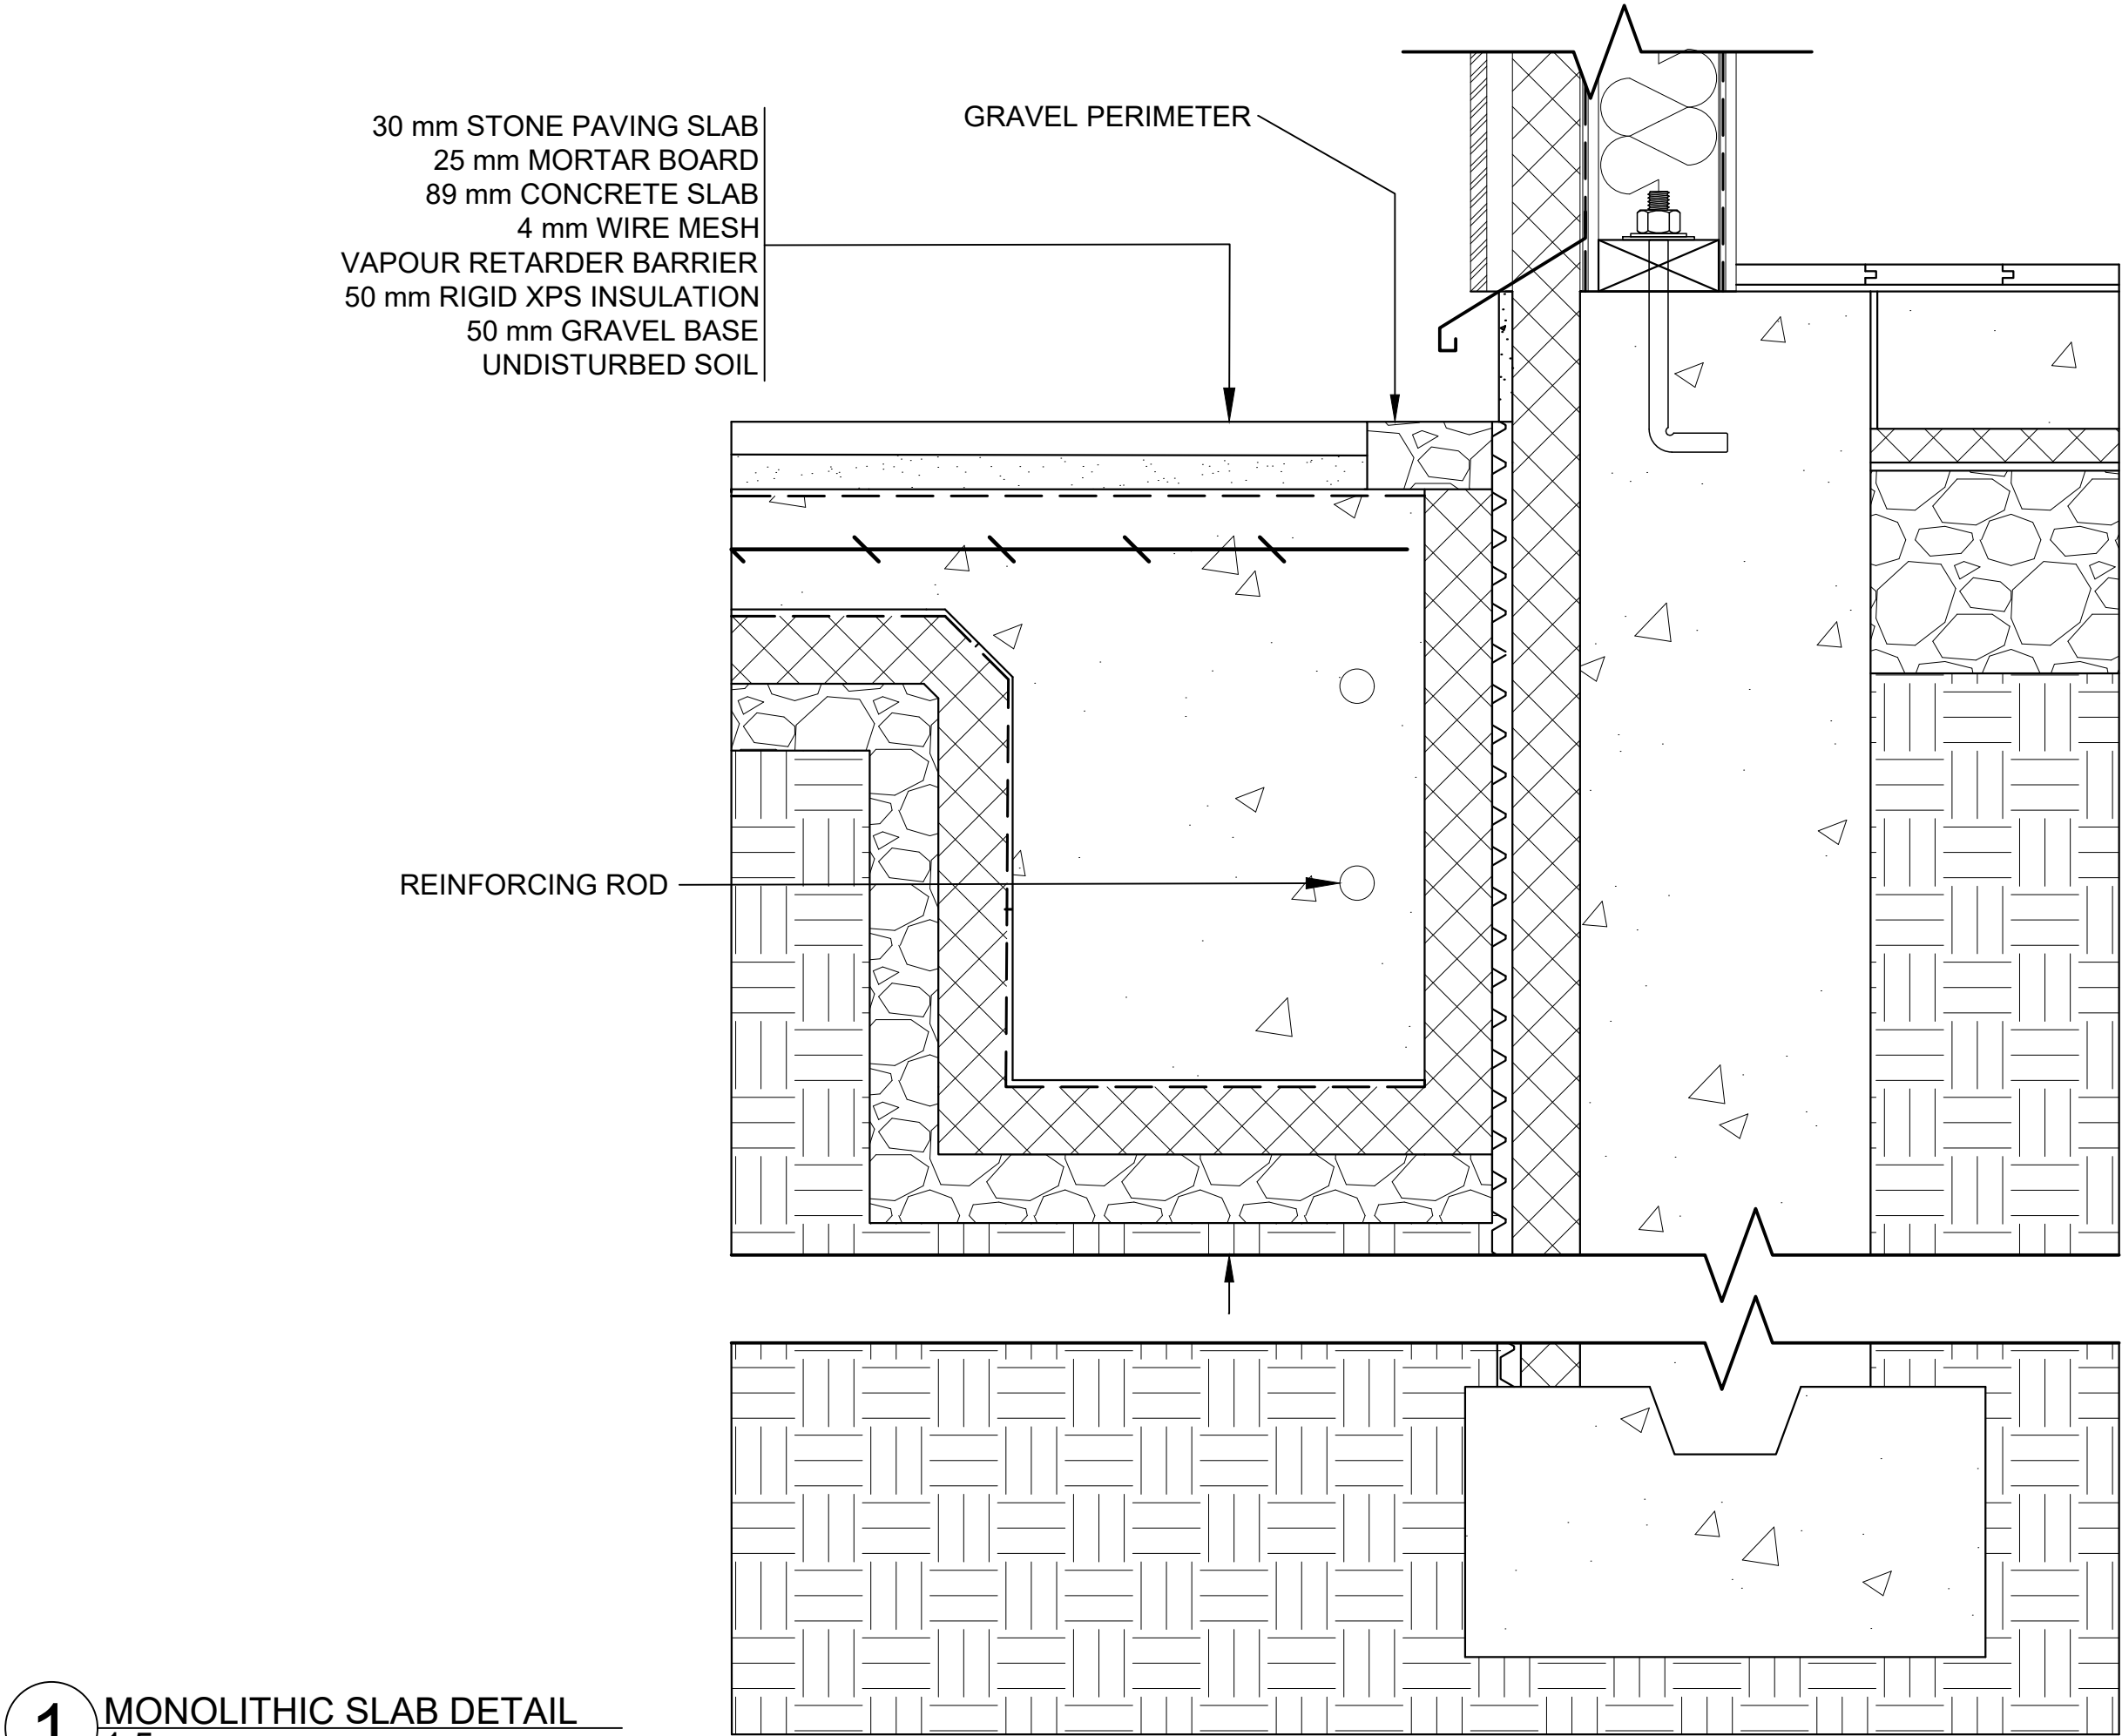

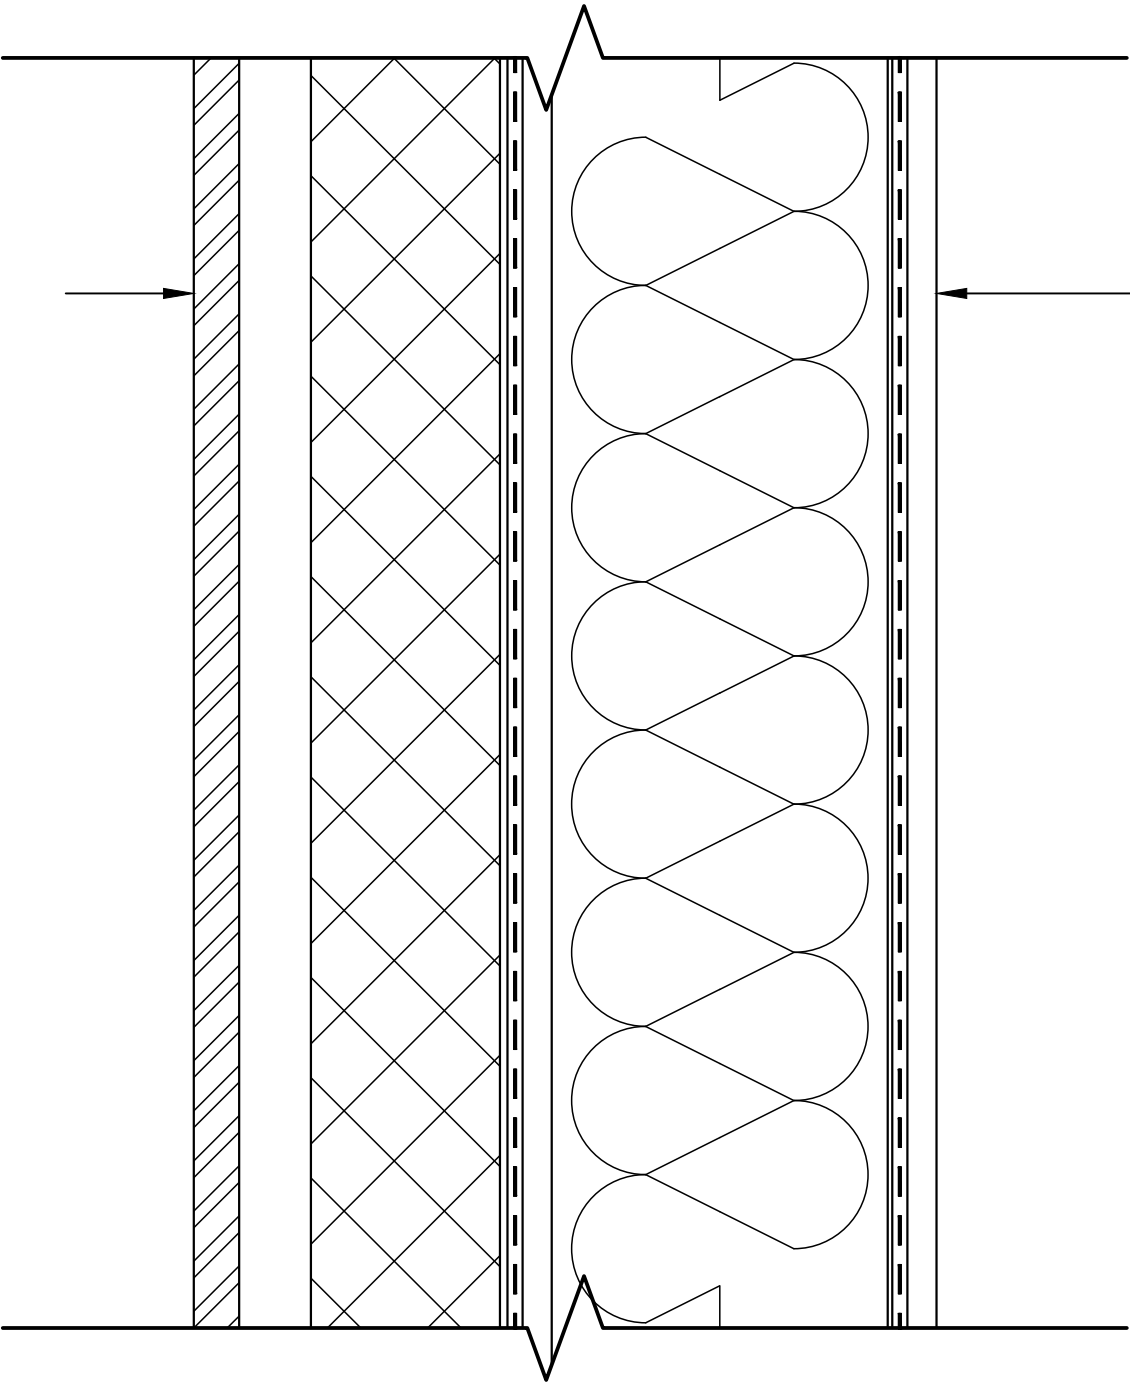

- 12 mm FIBRE CEMENT PANELS
- 130 FIBRE CEMENT SCREWS 292 mm APART
- 19 mm VENTILATED RAIN SCREEN
- 50 mm GRAPHITE EPS - RIGID INSULATION
- WEATHER RESISTIVE HOUSEWRAP
- 13 mm PLYWOOD SHEATHING
- 38 x 89 mm STUD AT 406 mm O.C.,
COMFORTBATT INSULATION INFILL
- SMART VAPOUR RETARDER
- 13 mm INTERIOR DRYWALL FINISH
- ACRYLIC PRIMER
- ACRYLIC LATEX PAINT



TINY RETREAT
PROJECT

WALL DETAIL


12/05/2025

mm

GROUP 8

1:2

AE403

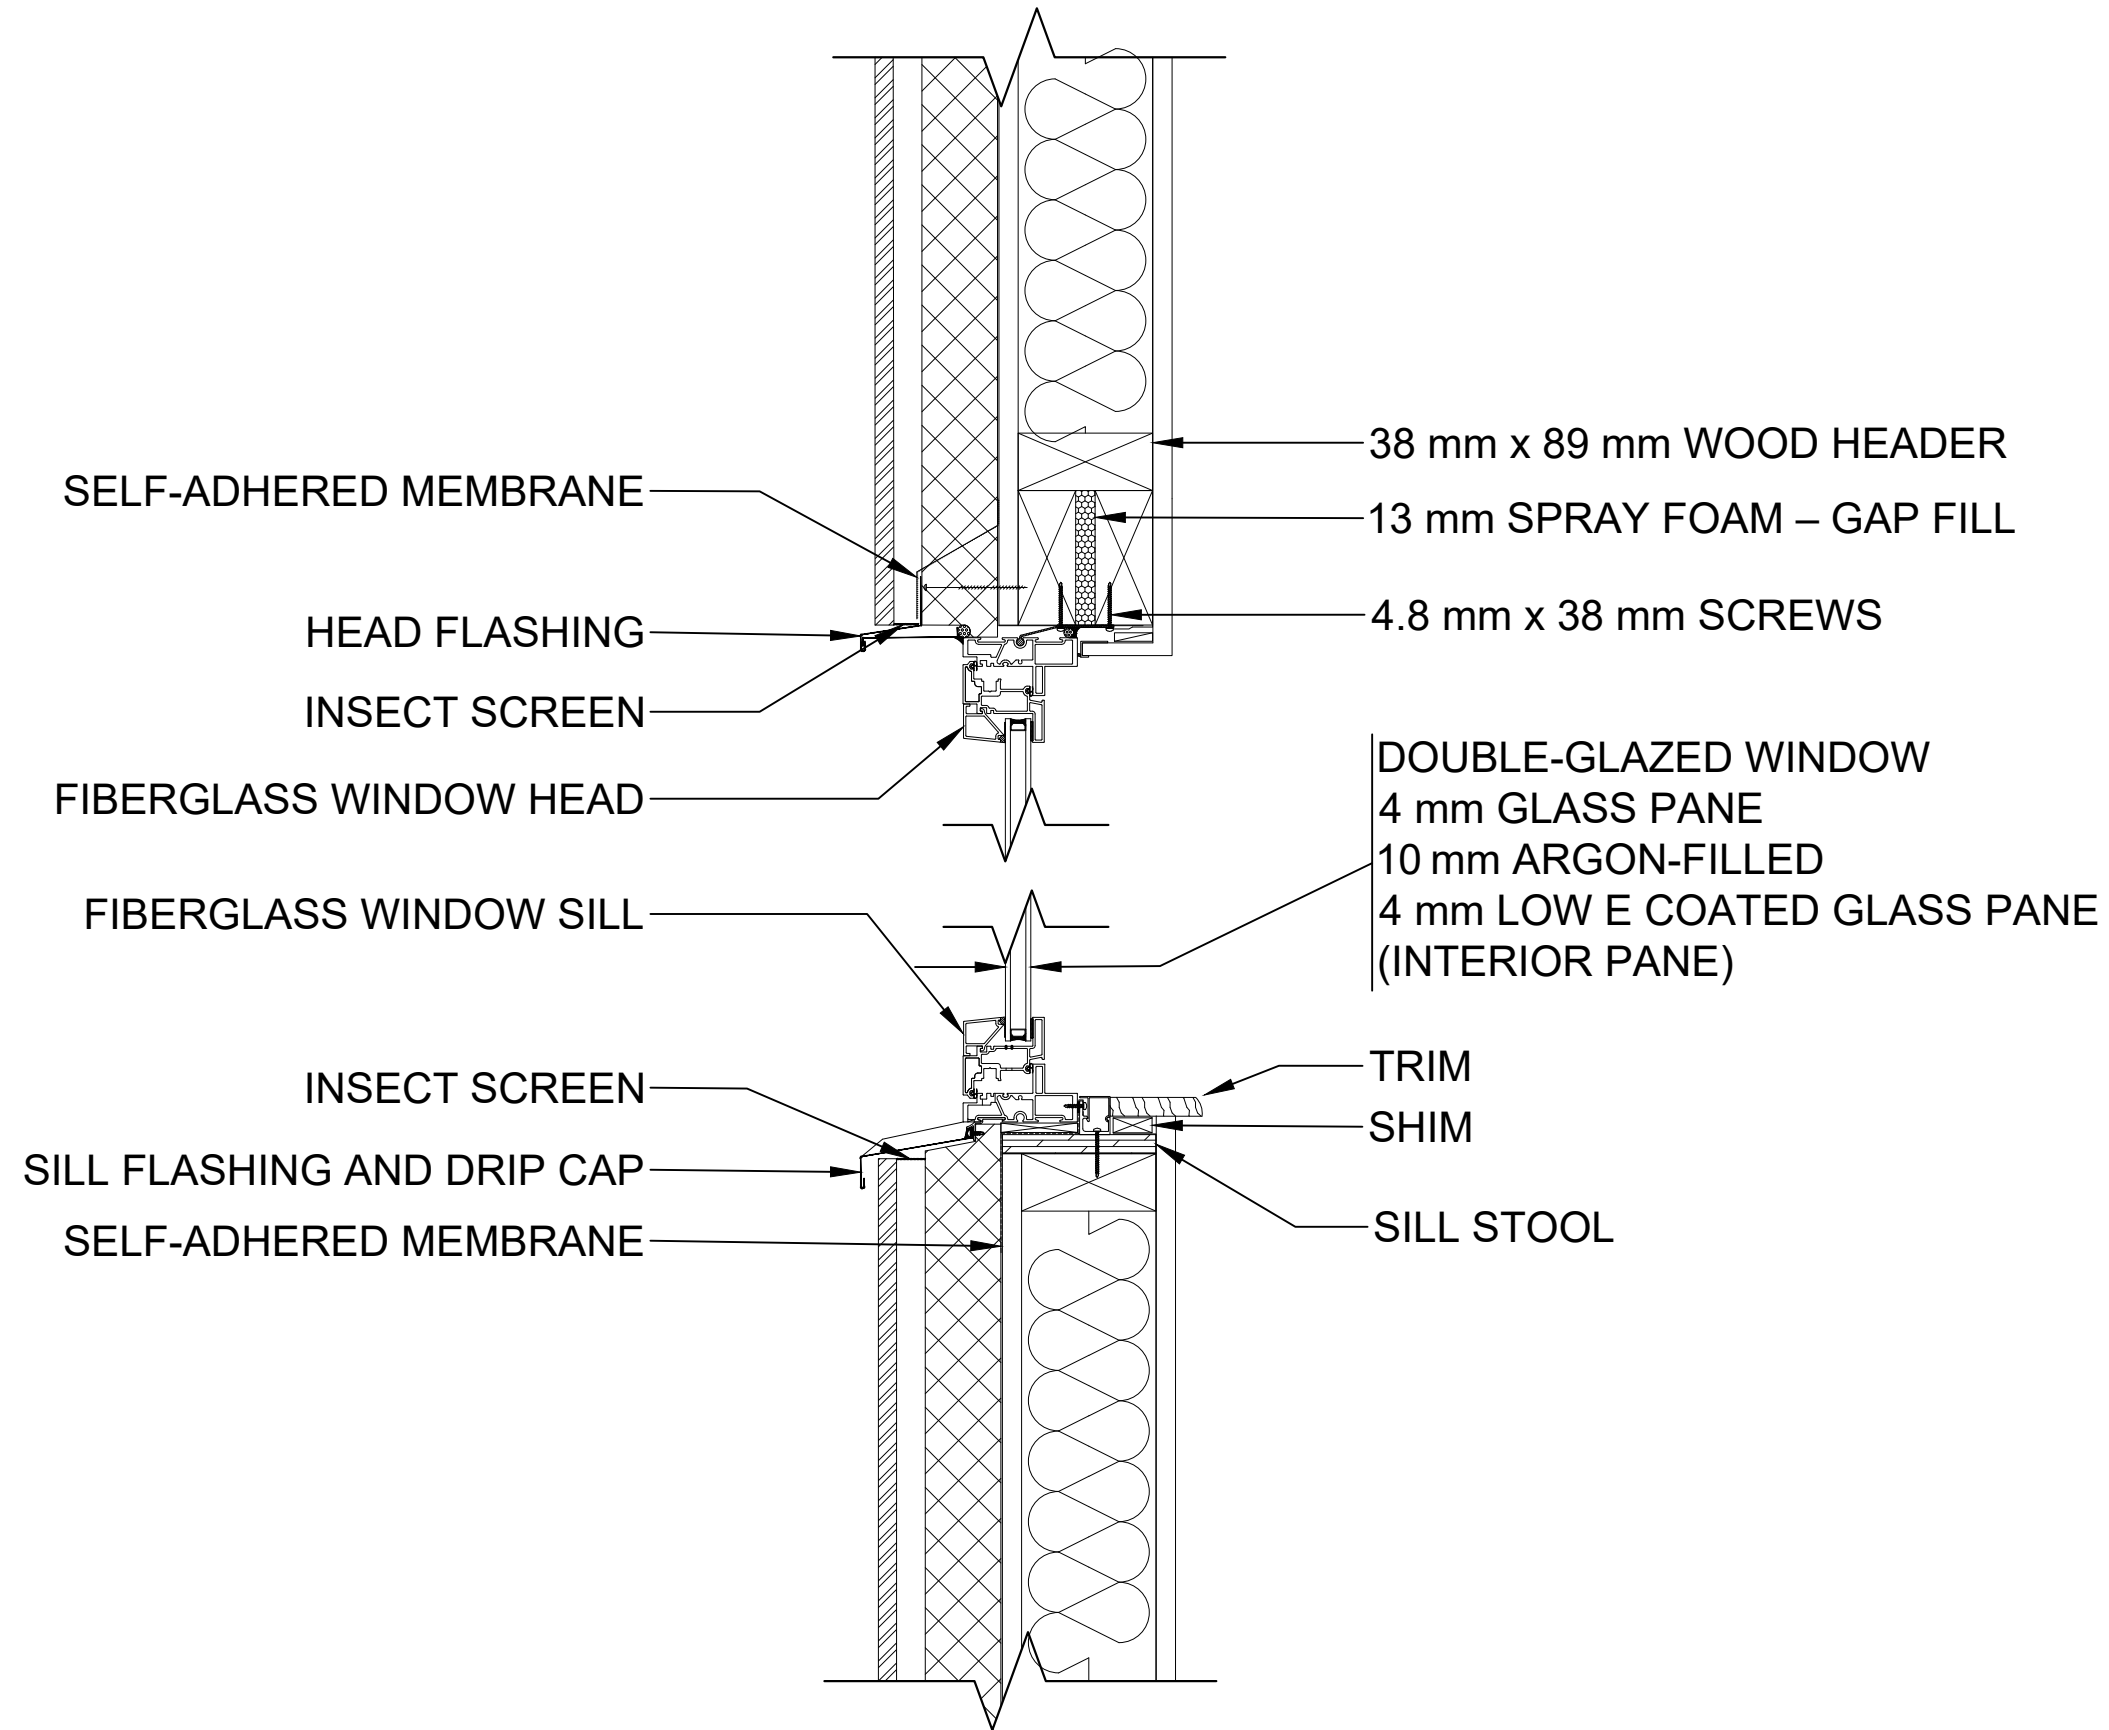

TINY RETREAT
PROJECT

WINDOW TO
WALL DETAIL

12/05/2025

mm

GROUP 8

1:5

AE404



TINY RETREAT PROJECT

PATIO DOOR DETAIL


12/05/2025

mm

GROUP 8

1:5

AE405

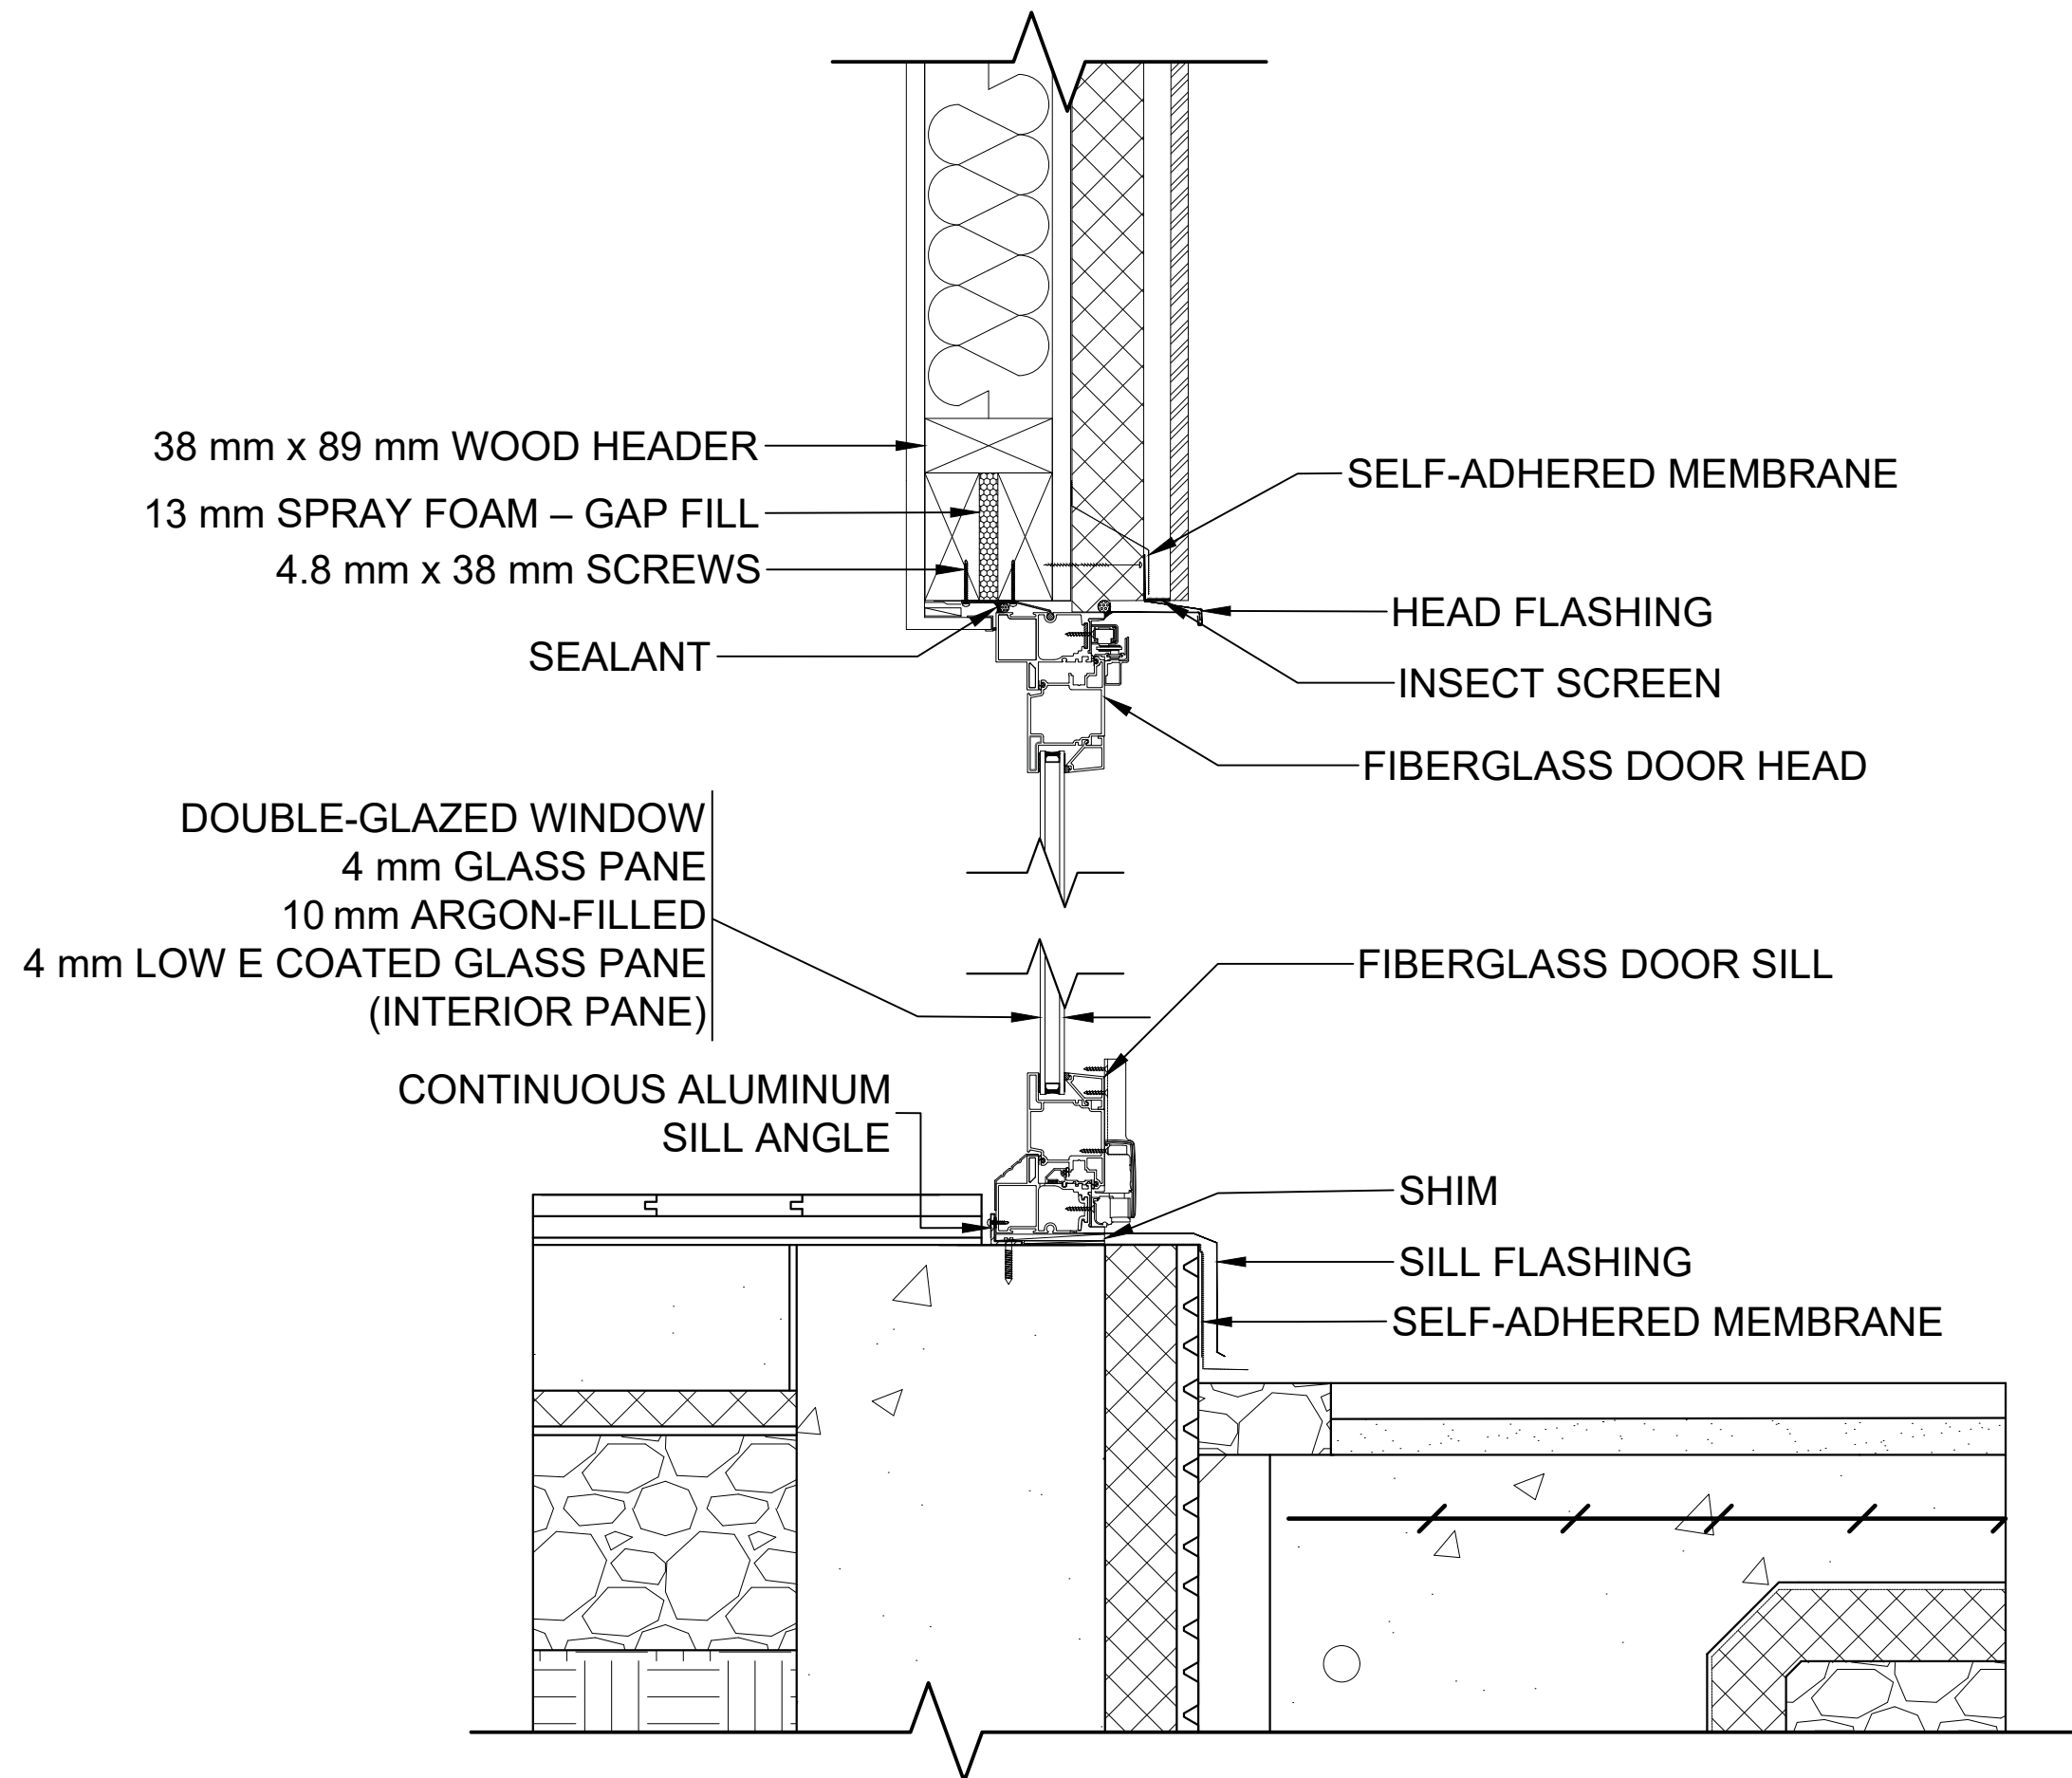

38 mm x 89 mm WOOD HEADER

13 mm SPRAY FOAM – GAP FILL

4.8 mm x 38 mm SCREWS

SEALANT

SELF-ADHERED MEMBRANE

HEAD FLASHING

INSECT SCREEN

FIBERGLASS DOOR HEAD

DOUBLE-GLAZED WINDOW

4 mm GLASS PANE

10 mm ARGON-FILLED

4 mm LOW E COATED GLASS PANE
(INTERIOR PANE)

FIBERGLASS DOOR SILL

CONTINUOUS ALUMINUM
SILL ANGLE

SHIM

SILL FLASHING

SELF-ADHERED MEMBRANE



TINY RETREAT
PROJECT

ROOF TO WALL
CONNECTION
DETAIL

12/05/2025

mm

GROUP 8

1:5

AE406

25mm STANDING SEAM METAL ROOF
19mm x 89mm STRAPPING
1mm ICE AND WATER SHIELD
13mm PLYWOOD SHEATHING
38mm x 140mm WOOD ROOF JOISTS,
COMFORTBATT INSULATION INFILL
SMART VAPOUR RETARDER
13 mm INTERIOR DRYWALL FINISH

FLASHING

2-38mm x 241mm BEAM

RAFTER HANGER

METAL ATTACHED TO
STRAPPING BY STANDING
SEAM ROOF CLIPS

DRIP EDGE FLASHING

38mm x 140mm FASCIA

FASCIA TRIM

ALUMINUM SOFFIT

J CHANNEL

38mm x 89mm RAFTER BLOCKING

76mm SEAT CUT
44mm HEEL CUT

GENERAL NOTES:

- CLOSED-CELL BACKER ROD IS TO BE INSTALLED UNDER CENTER OF EACH STANDING SEAM METAL PANEL FOR ADDITIONAL SUPPORT AND TO REDUCE OIL CANNING
- 19mm x 89mm STRAPPING IS TO BE INSTALLED ANGLED TO PREVENT WATER ACCUMULATION BENEATH METAL

1

ROOF TO WALL CONNECTION
1:5



TINY RETREAT
PROJECT

FENCE POST
DETAIL


12/05/2025

mm

GROUP 8


1:5

AE407

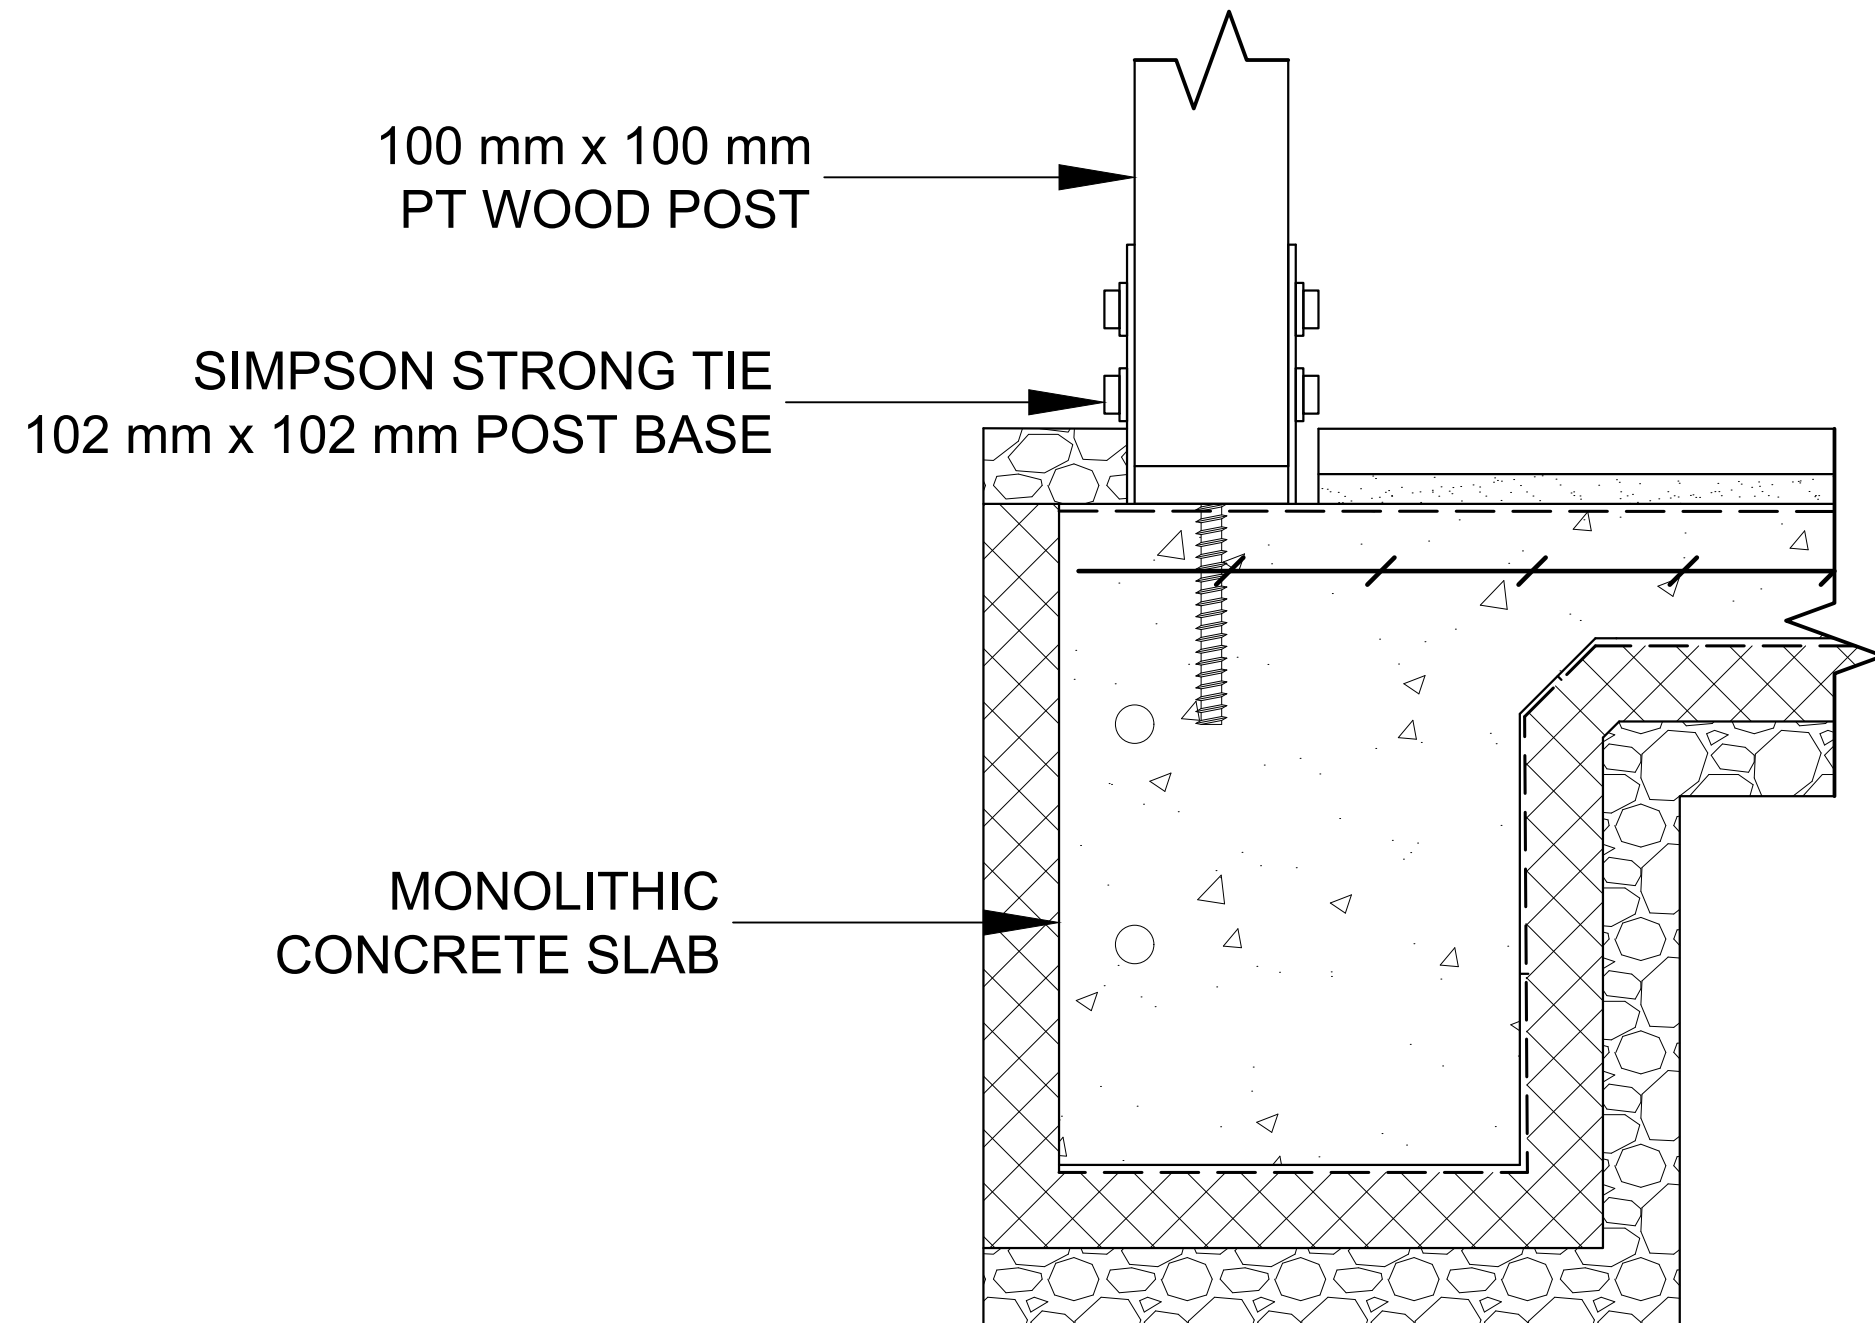


GENERAL NOTES:

- MARINE-GRADE OR EXTERIOR TWO-PART EPOXY IS TO BE USED IN LOUVER AND BEAM PIN HOLES TO SECURE STAINLESS STEEL PINS

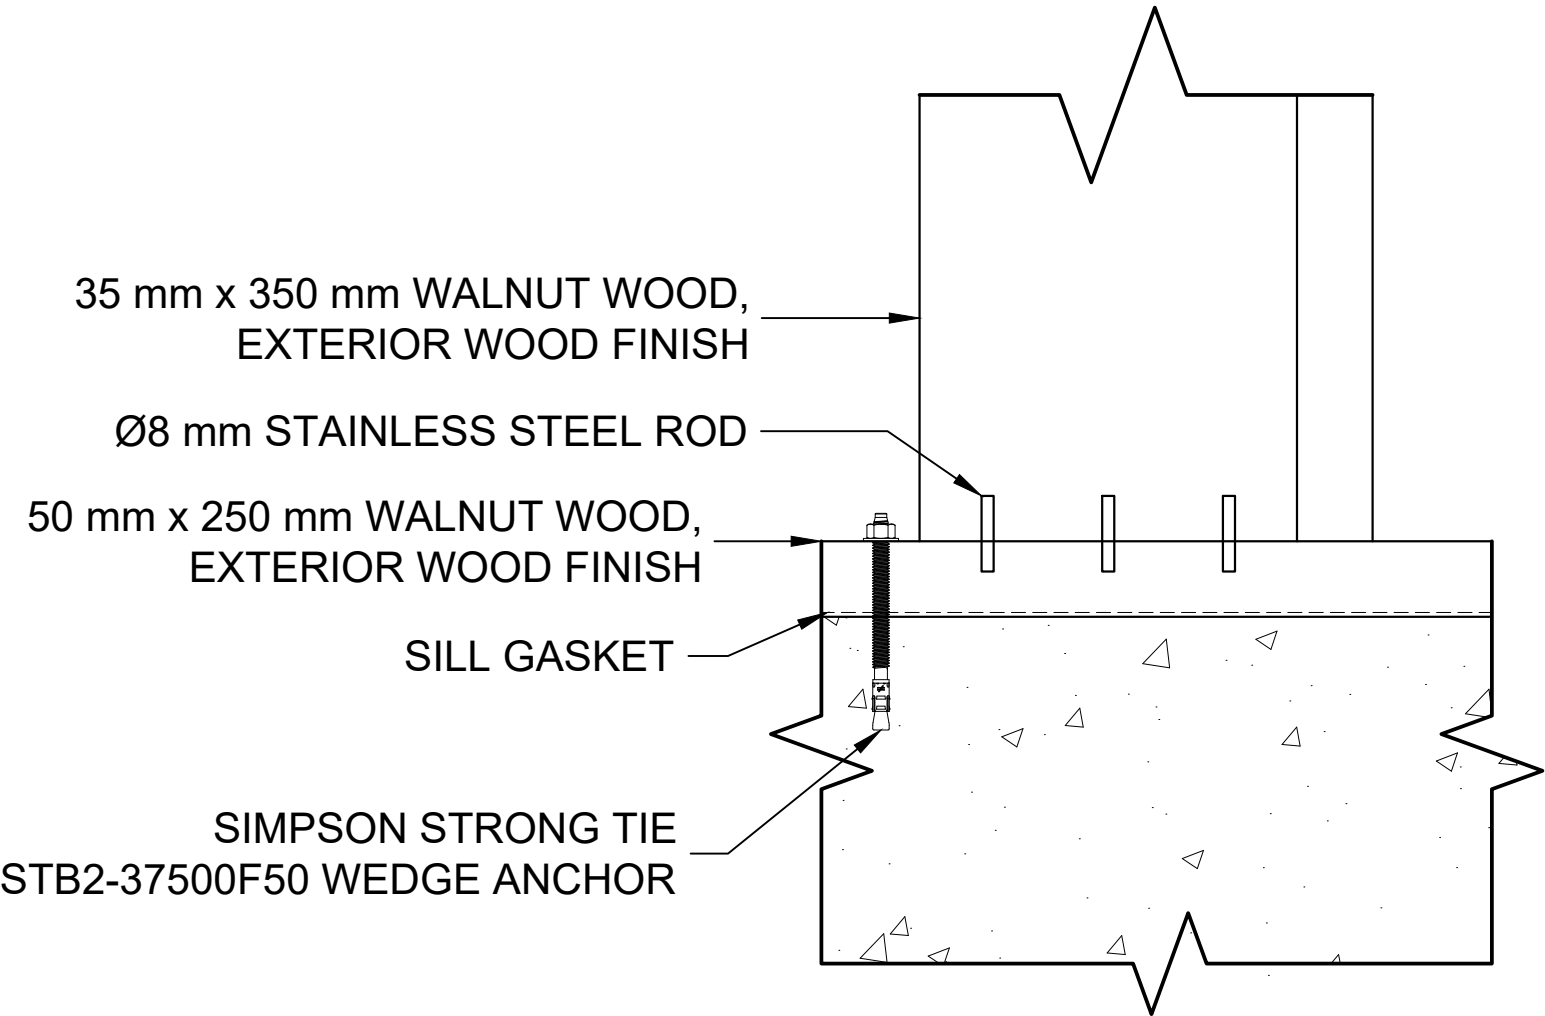

1 LOUVER TO SLAB CONNECTION
1:5

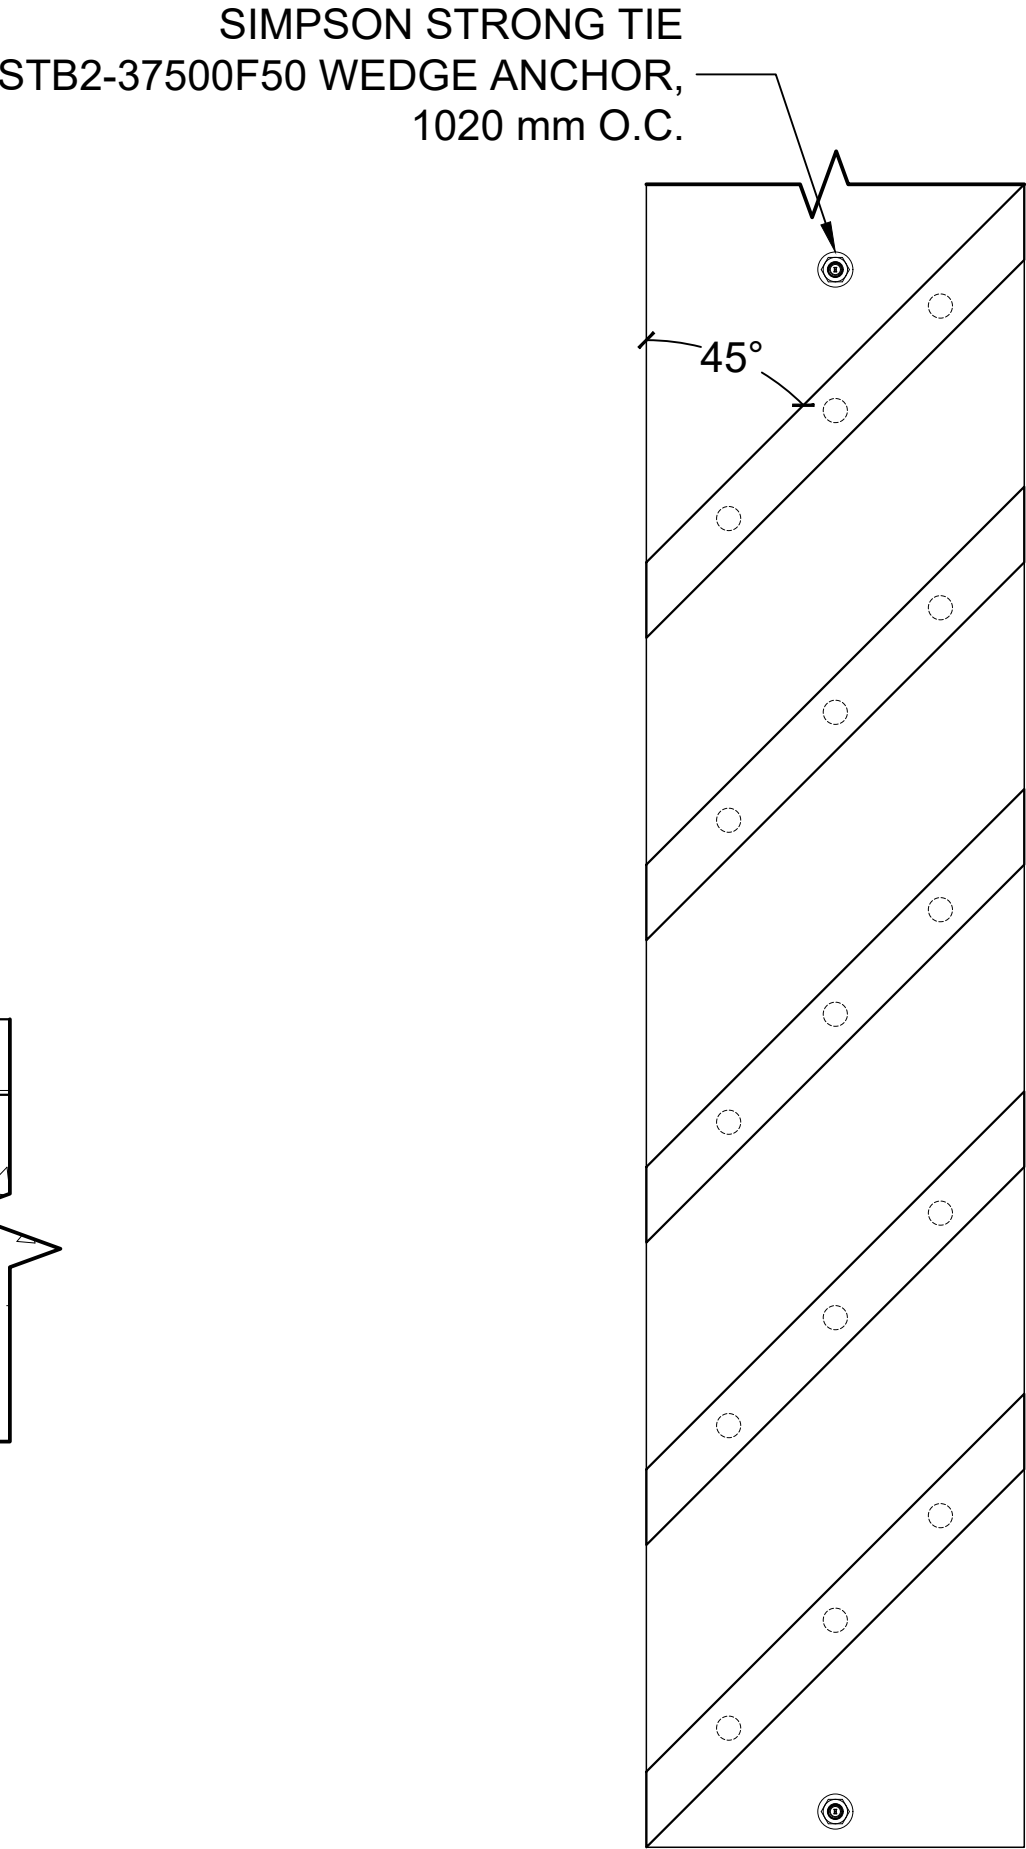

2 LOUVER PLAN VIEW
1:5



190 Westmount Rd N,
Waterloo, ON N2L 3G5



TINY RETREAT
PROJECT

LOUVER DETAIL

12/05/2025

mm

GROUP 8

1:5

AE408